
SHEET 1 – OVERALL MAP: FROM THE MAIN ROAD TO THE COLONY

Existing Jalkoti–Maheshwar road → 553 m approach road (15 m, over the bridge) → main entry → 223 m access road through the resort (15 m) → colony gate.

Total from the main road to the colony gate ≈ 800 m. All colony roads are 12 m; the farthest plot (V43) is 360 m inside the gate.

The approach road and the access road should both be dedicated as public roads (gift deed / record) before the colony application.

Approach road, bridge, existing road and mandir traced from the survey (Drg SU/10/01, 1:1000); widths read off its road lines and road section.

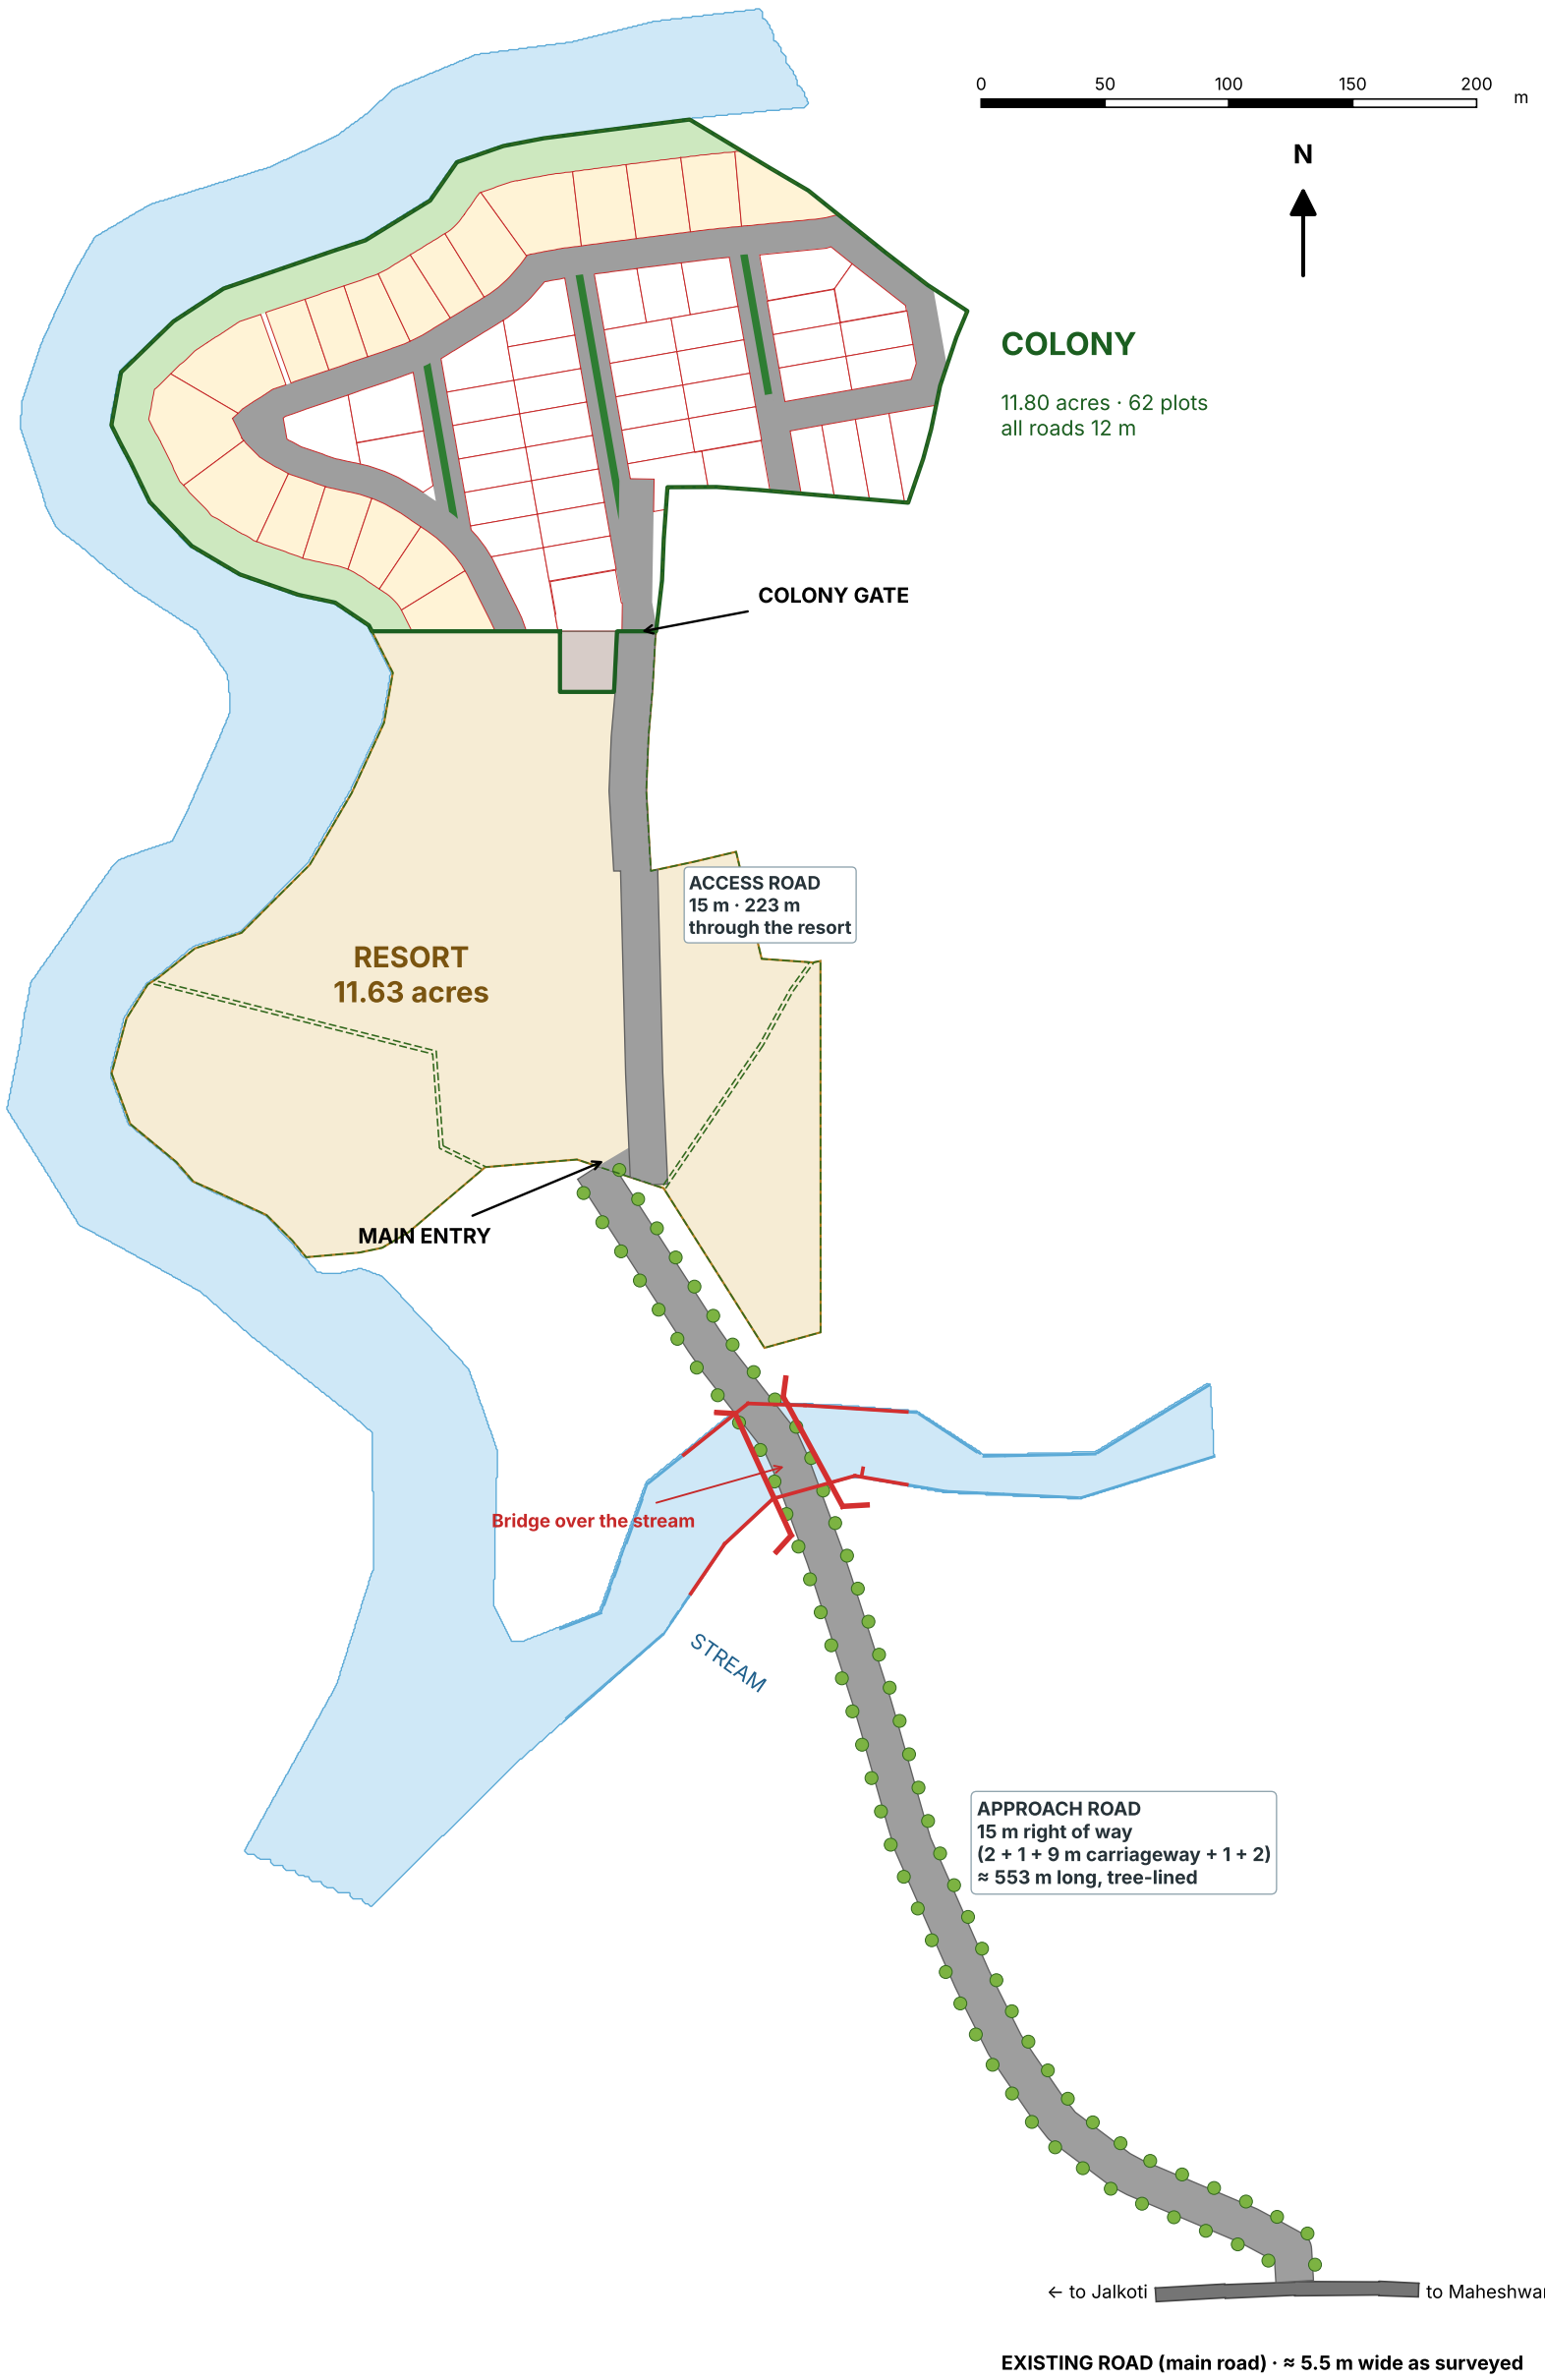

JALKOTI COLONY – MAHESHWAR (Khargone, MP)

Survey Drg SU/10/01 · 23.325 acres · colony 11.80 ac + resort 11.63 ac

Overall map – main road to colony

Approach road, main entry, access road and colony

Sheet 1 of 9

Concept – not an approved drawing

Scale 1:3000 on A3 · 12 Nov 2026



COLONY LAYOUT

62 plots · all roads 12 m · S1 joined to S2 by the S5 link road

AREA STATEMENT

Use	No.	sq ft	m²	%
River-front plots	19	134,511	12,496	26.2
Villa plots	43	190,872	17,732	37.1
Roads – carriageway and verges		109,048	10,131	21.2
Garden medians (road land)		6,821	634	1.3
Riverside garden (open space)		66,261	6,156	12.9
Services plot		5,906	549	1.1
Landscaped corners		4,516	420	0.9
7 ft walkway		712	66	0.1
Total colony	62	513,947	47,747	100.0

SELLABLE 325,383 sq ft = 7.47 acres = 63.3% of the colony

Open space: riverside garden 12.9% (BVN minimum 10%)

PLOTS

- 19 river-front plots 5,275–10,853 sq ft (average 7,080), backing onto the riverside garden
- 43 villa plots 3,616–6,489 sq ft (average 4,439); typical 45 × 90 ft
- Every plot fronts a 12 m road; every frontage is above 12 m (BVN Rule 53)
- Full side dimensions: Sheets 3–7 and the schedule on Sheet 8

ROADS

- RD: 12 m, about 456 m – along the river-front plots, from S1 round the bend to the south end
- S1: 12 m, about 70 m – from RD (via the bend at V5/V7) down the east boundary to S5
- S2: 12 m, about 111 m – from RD south to the boundary (V38 stub)
- S3: 12 m, about 155 m – from RD south to the colony gate
- S4: 12 m, about 64 m – from RD south to the RD south loop
- S5: 12 m, about 68 m – joins S1 to S2 along V16/V18 (new)
- Access road: 15 m, about 223 m – colony gate to the main entry
- Garden medians 3.0 m wide on S2, S3, S4 (61 m, 100 m, 64 m)
- Dead ends: S2 stub (V38) 42 m and RD south end 66 m – straight, with a 12 × 11 m turning space

SERVICES AND OPEN SPACE

- Riverside garden 15 m wide, about 460 m along the plots, 6,156 m²
- 7 ft walkway from RD between R10 and R11: 2.13 × 31.3 m
- Services plot at the gate 24.5 × 23.2 m (549 m²): STP, overhead tank + tubewell, waste point

River-front plot
Villa plot
Road (right of way)
Garden median (road land)
Riverside garden (open space)
Landscaped corner
7 ft walkway
Services plot
T = turning space 12 × 11 m
Resort
Colony boundary

JALKOTI COLONY – MAHESHWAR (Khargone, MP)

Survey Drg SU/10/01 · 23.325 acres · colony 11.80 ac + resort 11.63 ac

Colony layout

Plot numbers and areas, roads and open spaces

Sheet 2 of 9

Scale 1:1000 on A2 · 12 Nov 2026

Concept – not an approved drawing

DIMENSIONED LAYOUT

Every plot side, road, garden median and open space · 62 plots

HOW TO READ

- Blue figures inside each plot: side lengths in feet (1 m = 3.281 ft)
- "arc" = curved side, length measured along the curve
- Bold figure: plot number and area in sq ft
- Road arrows: right-of-way width across the road (m)
- White text on green: garden median width × length (m)
- Green arrows across the riverside garden: its width (m)
- Dark-green figures outside the boundary: colony boundary lengths (m)
- T = turning space 12 × 11 m at a dead end

ROADS (all 12 m inside the colony)

- RD: 12 m ROW, about 456 m long
- S1: 12 m ROW, about 70 m long
- S2: 12 m ROW, about 111 m long
- S3: 12 m ROW, about 155 m long
- S4: 12 m ROW, about 64 m long
- S5: 12 m ROW, about 68 m long
- Access road: 15 m ROW, about 223 m long
- Plain 12 m road: 2.25 m verge + 7.5 m carriageway + 2.25 m verge
- Garden street 12 m: 1.0 m footpath + 3.5 m lane + 3.0 m median + 3.5 m lane + 1.0 m footpath

GARDEN MEDIANS

- On S2: 3.0 m × 61.0 m (172 m²)
- On S3: 3.0 m × 100.3 m (277 m²)
- On S4: 3.0 m × 63.9 m (185 m²)

OPEN SPACE AND SERVICES

- Riverside garden: 15 m wide, 460 m along the plots, 6,156 m²
- Walkway: 2.13 m (7 ft) × 31.3 m, between R10 and R11
- Services plot: 24.5 × 23.2 m (549 m²)
- STP 10 × 8 m · tank + tubewell 7 × 7 m · waste point 5 × 4 m
- Landscaped corners: 6 pieces, 420 m² in all

SETBACKS (BVN 2012, Rule 56)

- Front 3.6 m on a 12 m road · rear 3.0 m · sides 3.0 m each (detached)
- River-front plots: 15 m from the stream edge + 3 m rear setback

ACCURACY

- Measured from the survey scan (Drg SU/10/01) calibrated to its surveyed areas
- Expect ±0.5 m. Redraw on the CAD survey and
- verify on site before marking out or selling

AREA STATEMENT

Use	No.	sq ft	m²	%
River-front plots	19	134,511	12,496	26.2
Villa plots	43	190,872	17,732	37.1
Roads – carriageway and verges		109,048	10,131	21.2
Garden medians (road land)		6,821	634	1.3
Riverside garden (open space)		66,261	6,156	12.9
Services plot		5,906	549	1.1
Landscaped corners		4,516	420	0.9
7 ft walkway		712	66	0.1
Total colony	62	513,947	47,747	100.0

SELLABLE 325,383 sq ft · 63.3%

River-front plot
Villa plot
Road (right of way)
Garden median (road land)
Riverside garden (open space)
Landscaped corner
7 ft walkway
Services plot
T = turning space 12 × 11 m
Resort
Colony boundary

JALKOTI COLONY – MAHESHWAR (Khargone, MP)

Survey Drg SU/10/01 · 23.325 acres · colony 11.80 ac + resort 11.63 ac

Dimensioned layout – big map

All plot sides in feet; roads, medians, garden and boundary in metres


Sheet 3 of 9

Scale 1:400 on A0 · 12 Nov 2026

Concept – not an approved drawing

SHEET 4 – DIMENSIONS, NORTH-WEST QUARTER

Plot sides in feet (blue, inside each plot) · road widths, garden medians, garden and boundary in metres · areas in sq ft

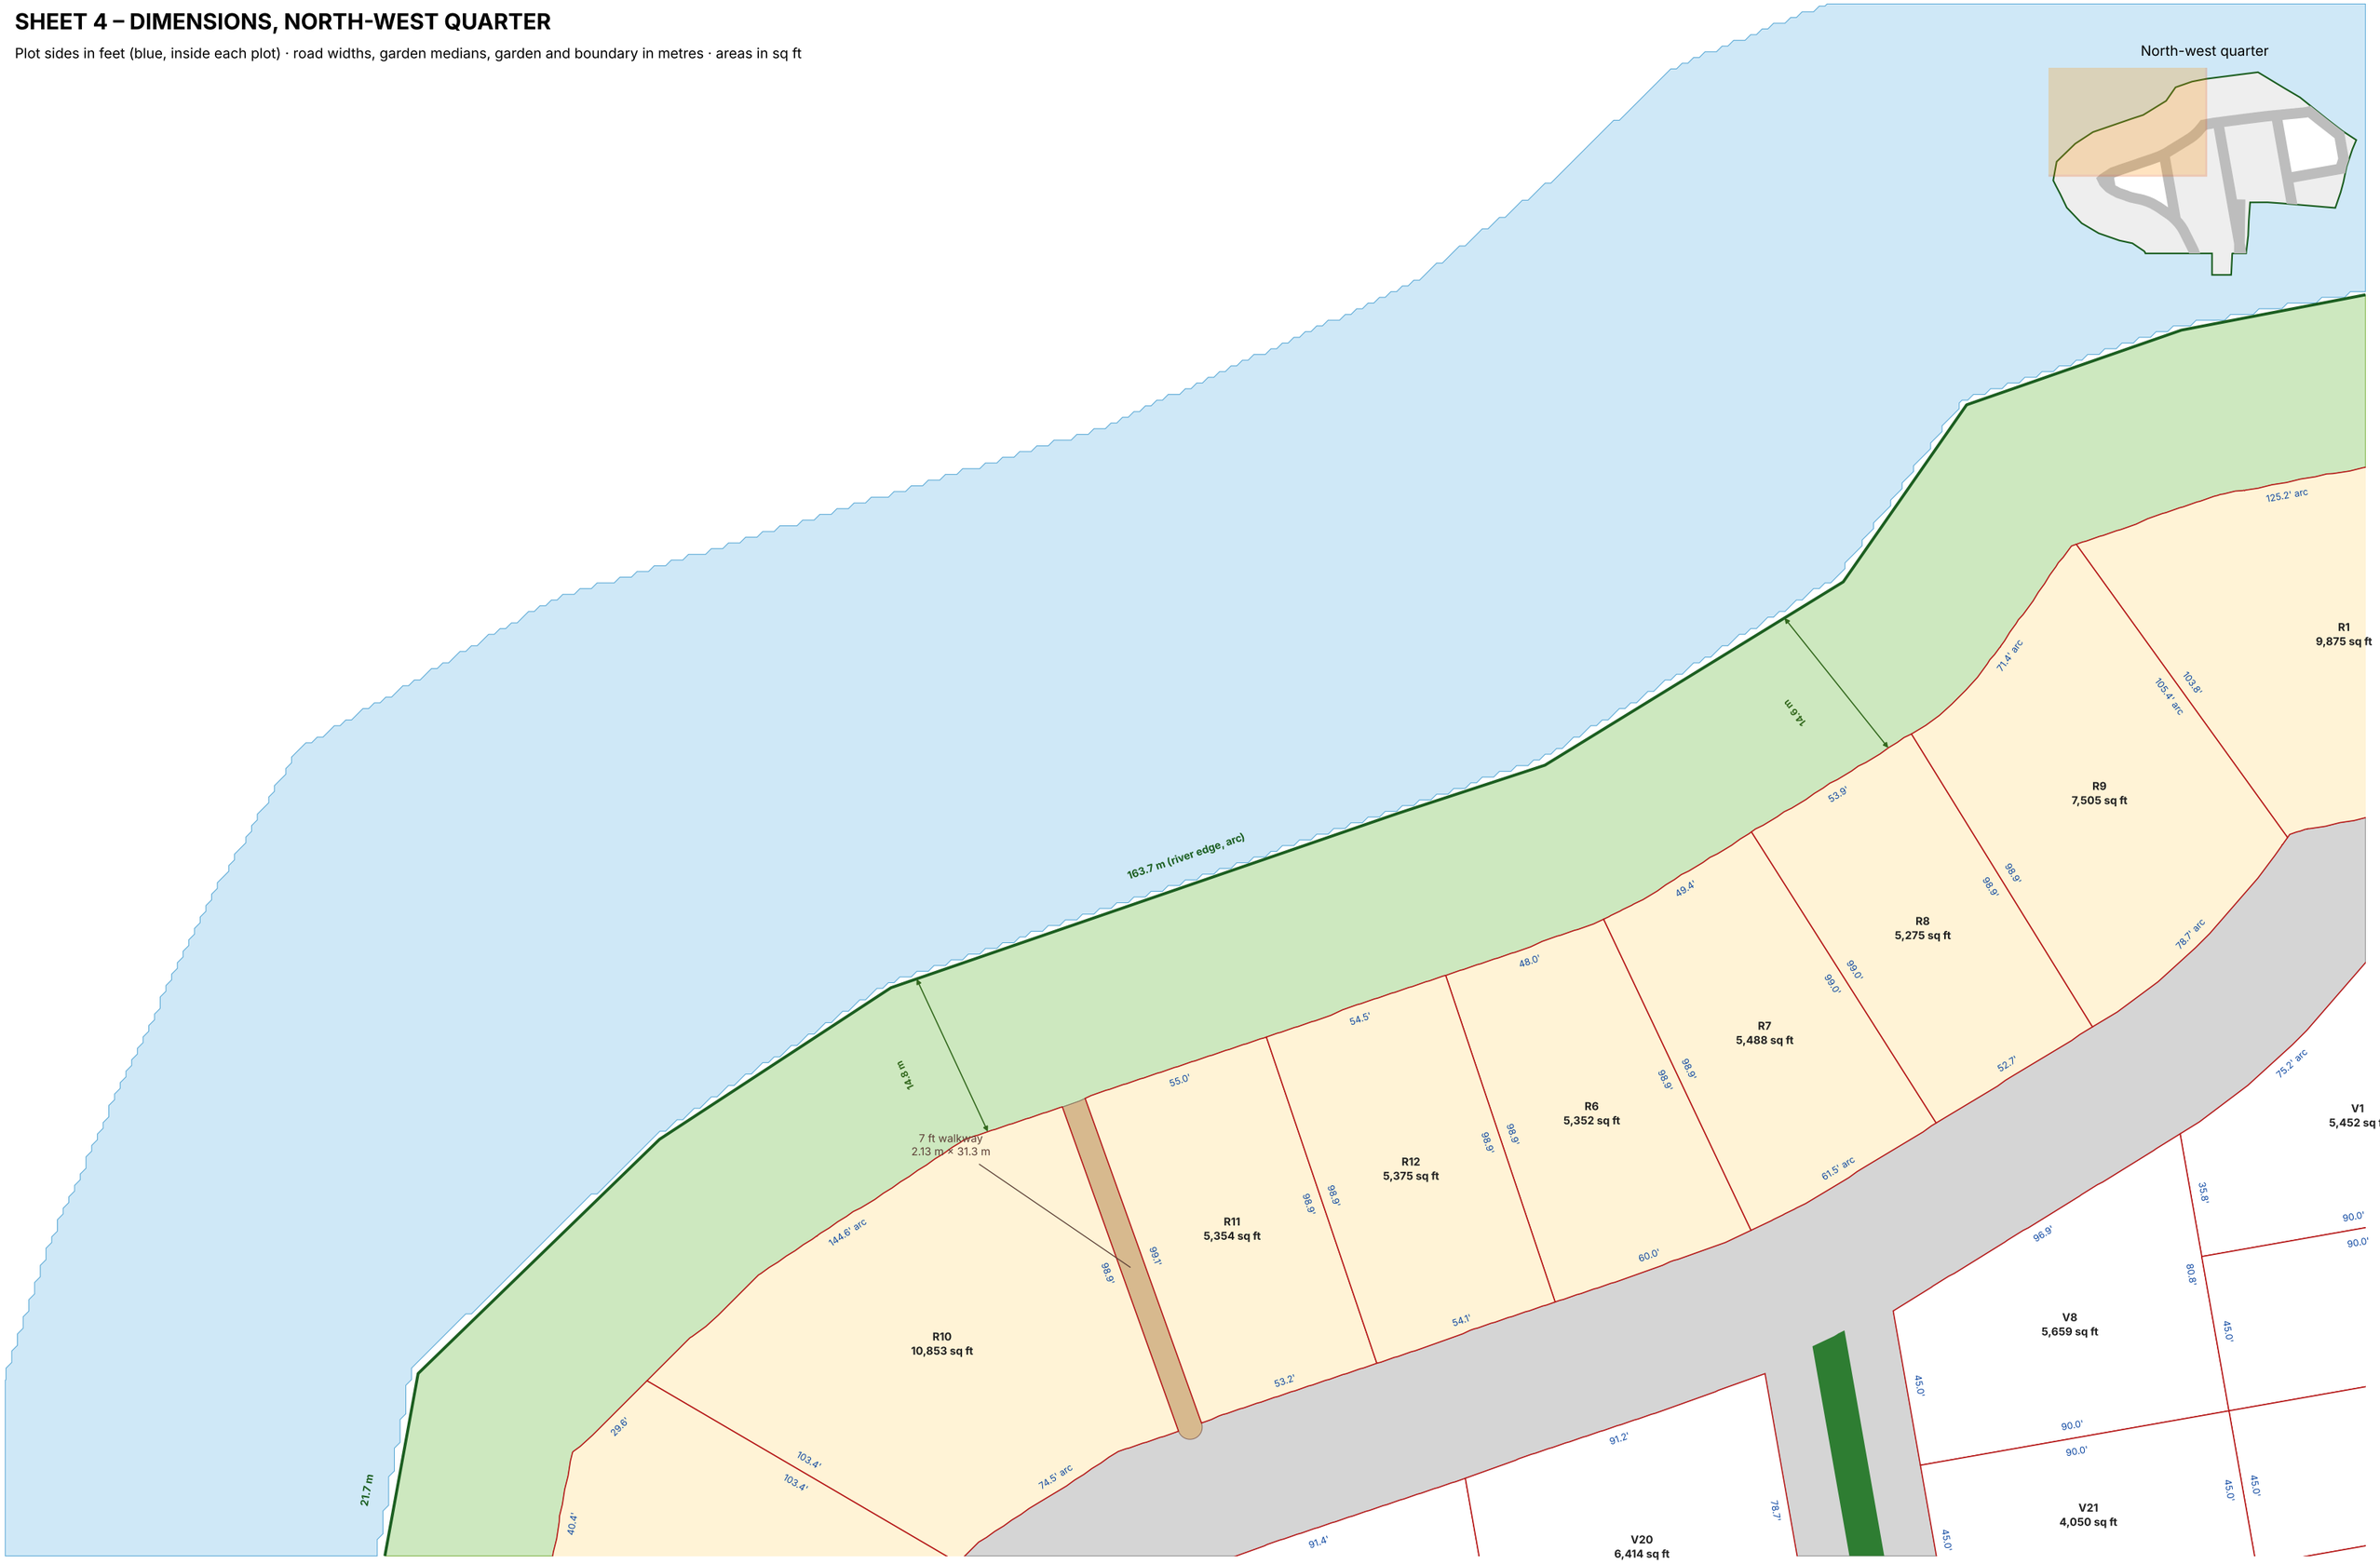

JALKOTI COLONY – MAHESHWAR (Khargone, MP)

Survey Drg SU/10/01 · 23.325 acres · colony 11.80 ac + resort 11.63 ac

Dimension sheet – north-west quarter

Plot sides (ft), roads, medians, garden and boundary (m)


Sheet 4 of 9

Scale 1:500 on A3 · 12 Nov 2026

Concept – not an approved drawing

SHEET 5 – DIMENSIONS, NORTH-EAST QUARTER

Plot sides in feet (blue, inside each plot) · road widths, garden medians, garden and boundary in metres · areas in sq ft

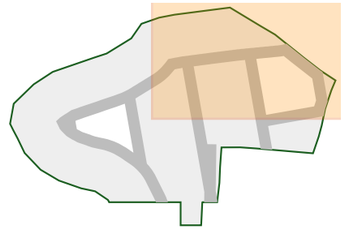

95.9 m (river edge, arc)
14.8 m
R1
9,875 sq ft
R2
7,170 sq ft
R3
7,193 sq ft
R4
6,943 sq ft
R5
7,351 sq ft
R9
7,505 sq ft
125.2' arc
71.5'
73.1'
72.3'
9.6'
152.2' arc
138.4 m arc
98.9'
98.9'
98.9'
99.3'
99.3'
99.1'
99.1'
103.8'
105.4' arc
74.3' arc
73.4'
72.3'
68.1'
128.2' arc
78.7' arc
V1
5,452 sq ft
V2
4,206 sq ft
V3
4,207 sq ft
V4
4,354 sq ft
V5
6,081 sq ft
V6
4,050 sq ft
V7
4,119 sq ft
V9
4,050 sq ft
V10
4,050 sq ft
V11
4,050 sq ft
V12
4,050 sq ft
V13
4,050 sq ft
V14
4,050 sq ft
V15
4,050 sq ft
V16
4,050 sq ft
V17
4,050 sq ft
V18
3,949 sq ft
V25
4,050 sq ft
V27
4,050 sq ft
27.3'
75.2' arc
76.8'
35.8'
80.8'
56.6'
59.0'
64.1'
75.1'
72.5'
72.5'
69.7'
69.7'
66.0'
56.9'
59.1'
64.0'
95.2' arc
36.0'
61.5'
42.5' arc
40.3'
87.7'
89.8'
45.3'
88.7'
47.6' arc
79.7'
63.3'
garden median 3.0 m × 100.3 m
garden median 3.0 m × 61.0 m
12.1 m
S1 · 12 m ROW · 70 m long
S2 · 12 m ROW · 111 m lo
81.1 m arc

JALKOTI COLONY – MAHESHWAR (Khargone, MP)

Survey Drg SU/10/01 · 23.325 acres · colony 11.80 ac + resort 11.63 ac

Dimension sheet – north-east quarter

Plot sides (ft), roads, medians, garden and boundary (m)


Sheet 5 of 9

Scale 1:500 on A3 · 12 Nov 2026

Concept – not an approved drawing

SHEET 6 – DIMENSIONS, SOUTH-WEST QUARTER

Plot sides in feet (blue, inside each plot) · road widths, garden medians, garden and boundary in metres · areas in sq ft

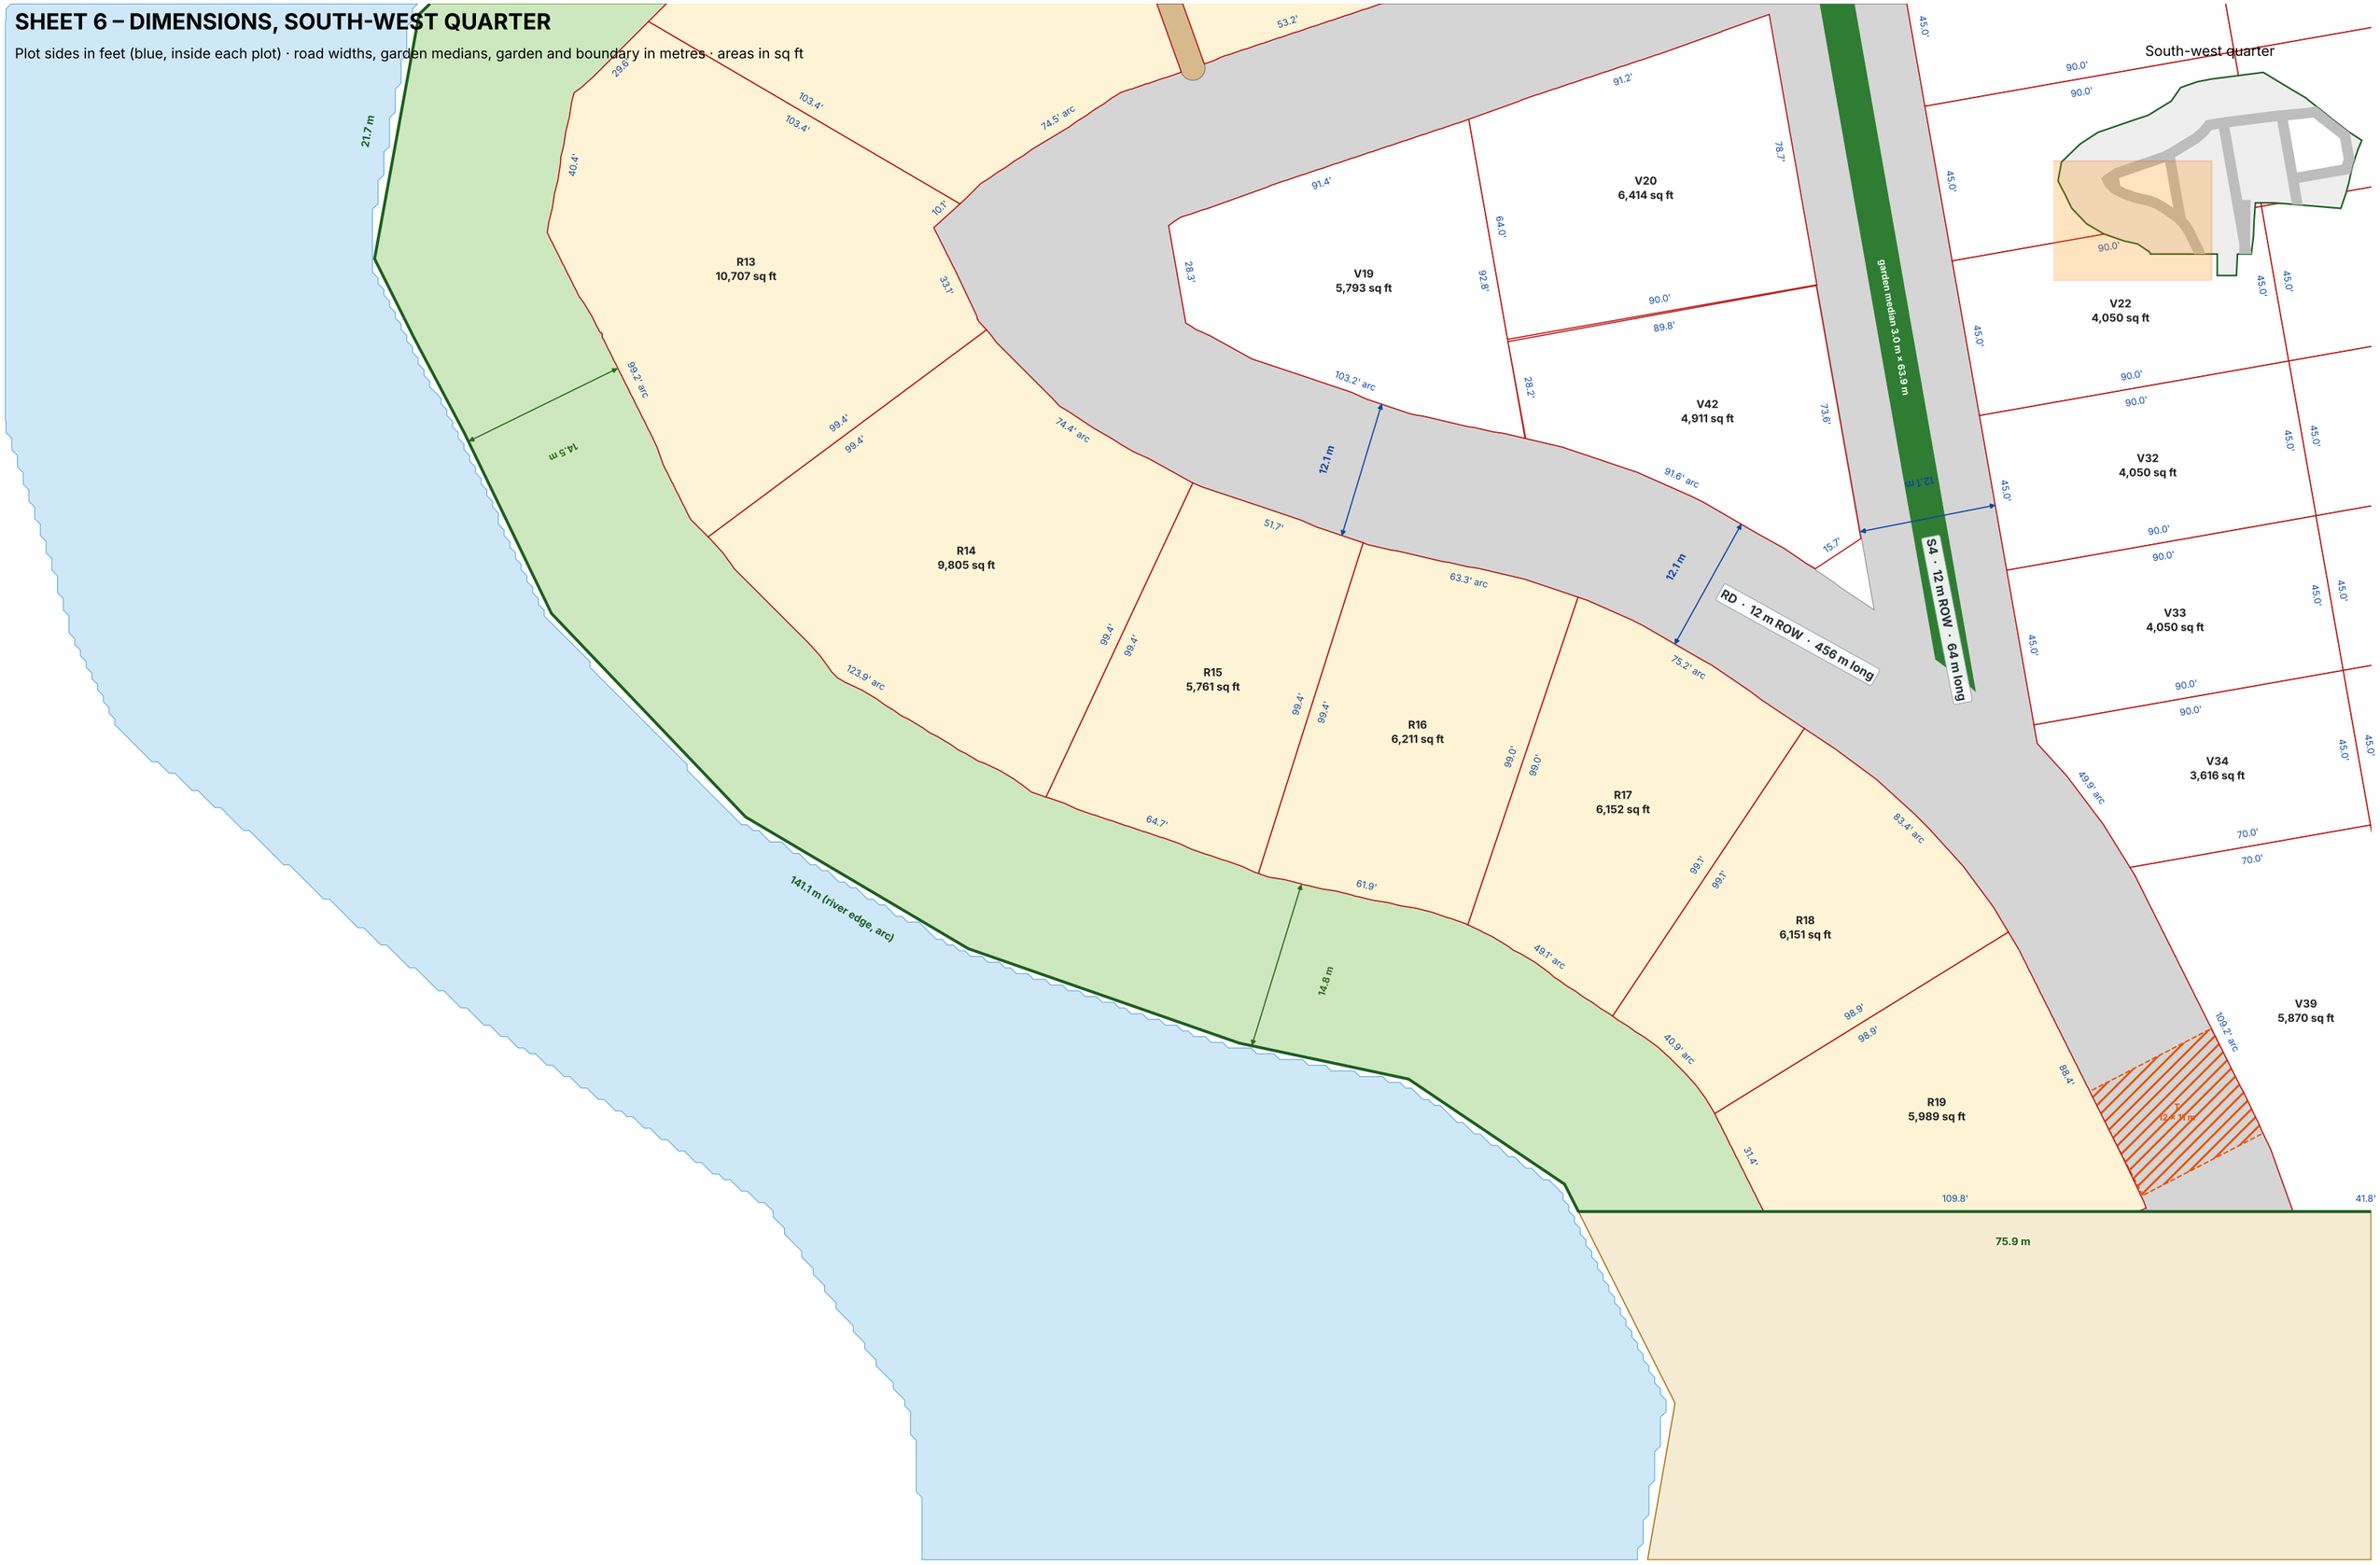

JALKOTI COLONY – MAHESHWAR (Khargone, MP)

Survey Drg SU/10/01 · 23.325 acres · colony 11.80 ac + resort 11.63 ac

Dimension sheet – south-west quarter

Plot sides (ft), roads, medians, garden and boundary (m)

Sheet 6 of 9

Scale 1:500 on A3 · 12 Nov 2026

Concept – not an approved drawing

SHEET 7 – DIMENSIONS, SOUTH-EAST QUARTER

Plot sides in feet (blue, inside each plot) · road widths, garden medians, garden and boundary in metres · areas in sq ft

South-east quarter

V10
4,050 sq ft

V12
4,050 sq ft

V16
4,050 sq ft

V22
4,050 sq ft

V23
4,050 sq ft

V24
4,050 sq ft

V25
4,050 sq ft

V26
4,050 sq ft

V27
4,050 sq ft

V28
4,050 sq ft

V29
3,835 sq ft

V30
4,592 sq ft

V31
5,133 sq ft

V32
4,050 sq ft

V33
4,050 sq ft

V34
3,616 sq ft

V35
4,050 sq ft

V36
4,050 sq ft

V37
4,181 sq ft

V38
4,522 sq ft

V39
5,870 sq ft

V40
4,050 sq ft

V41
6,489 sq ft

V43
4,340 sq ft

Garden median 3.0 m × 100.3 m

S3 · 12 m ROW · 155 m long

S2 · 12 m ROW · 111 m long

12 m

14 × 11 m

97.4 m arc

58.4 m arc

134.5' arc

108.2' arc

82.2' arc

12 × 11 m

COLONY GATE

W

STP

OHT

24.5 m

24.4 m

15.7 m

15.0 m

21.8 m

S · 223 m long

Concept – not an approved drawing

SHEET 8 – PLOT DIMENSION SCHEDULE

Sides run clockwise from the main road side (the front). Road sides carry the road name; "arc" = curved side measured along the curve.

Areas and lengths are measured from the calibrated survey scan (±0.5 m) – redraw on the CAD survey and verify on site before marking out.

Plot	Type	sq ft	m²	Road frontage	Sides in feet (clockwise from the front)	Sides in metres
R1	River-front	9,875	917.4	22.6 m · RD	74.3 RD arc · 103.8 · 125.2 arc · 98.9	22.65 RD arc · 31.64 · 38.17 arc · 30.15
R2	River-front	7,170	666.1	22.4 m · RD	73.4 RD · 98.9 · 71.5 · 98.9	22.37 RD · 30.15 · 21.78 · 30.14
R3	River-front	7,193	668.2	22.0 m · RD	72.3 RD · 98.9 · 73.1 · 99.3	22.04 RD · 30.14 · 22.27 · 30.25
R4	River-front	6,943	645.1	20.7 m · RD	68.1 RD · 99.3 · 72.3 · 99.1	20.74 RD · 30.25 · 22.03 · 30.21
R5	River-front	7,351	682.9	39.1 m · RD	128.2 RD arc · 99.1 · 9.6 · 152.2 arc	39.08 RD arc · 30.21 · 2.93 · 46.39 arc
R6	River-front	5,352	497.2	18.3 m · RD	60.0 RD · 98.9 · 48.0 · 98.9	18.28 RD · 30.15 · 14.64 · 30.14
R7	River-front	5,488	509.8	18.8 m · RD	61.5 RD arc · 98.9 · 49.4 · 99.0	18.76 RD arc · 30.14 · 15.04 · 30.18
R8	River-front	5,275	490.1	16.1 m · RD	52.7 RD · 99.0 · 53.9 · 98.9	16.07 RD · 30.18 · 16.42 · 30.14
R9	River-front	7,505	697.2	24.0 m · RD	78.7 RD arc · 98.9 · 71.4 arc · 105.4 arc	23.99 RD arc · 30.13 · 21.76 arc · 32.11 arc
R10	River-front	10,853	1,008.2	22.7 m · RD	74.5 RD arc · 103.4 · 144.6 arc · 98.9	22.71 RD arc · 31.52 · 44.09 arc · 30.16
R11	River-front	5,354	497.4	16.2 m · RD	53.2 RD · 99.1 · 55.0 · 98.9	16.22 RD · 30.19 · 16.75 · 30.15
R12	River-front	5,375	499.4	16.5 m · RD	54.1 RD · 98.9 · 54.5 · 98.9	16.50 RD · 30.15 · 16.60 · 30.15
R13	River-front	10,707	994.7	13.2 m · RD	33.1 RD · 99.4 · 99.2 arc · 40.4 · 29.6 · 103.4 · 10.1 RD	10.09 RD · 30.29 · 30.24 arc · 12.32 · 9.03 · 31.52 · 3.09 RD
R14	River-front	9,805	910.9	22.7 m · RD	74.4 RD arc · 99.4 · 123.9 arc · 99.4	22.67 RD arc · 30.29 · 37.76 arc · 30.29
R15	River-front	5,761	535.2	15.8 m · RD	51.7 RD · 99.4 · 64.7 · 99.4	15.77 RD · 30.29 · 19.71 · 30.29
R16	River-front	6,211	577.0	19.3 m · RD	63.3 RD arc · 99.0 · 61.9 · 99.4	19.31 RD arc · 30.18 · 18.86 · 30.29
R17	River-front	6,152	571.5	22.9 m · RD	75.2 RD arc · 99.1 · 49.1 arc · 99.0	22.91 RD arc · 30.19 · 14.97 arc · 30.18
R18	River-front	6,151	571.4	25.4 m · RD	83.4 RD arc · 98.9 · 40.9 arc · 99.1	25.42 RD arc · 30.15 · 12.48 arc · 30.19
R19	River-front	5,989	556.4	27.0 m · RD	88.4 RD · 109.8 · 31.4 · 98.9	26.96 RD · 33.46 · 9.56 · 30.15
V1	Villa	5,452	506.5	54.6 m · RD+S3	76.8 S3 · 90.0 · 35.8 · 75.2 RD arc · 27.3 RD	23.41 S3 · 27.43 · 10.91 · 22.91 RD arc · 8.32 RD
V2	Villa	4,206	390.8	40.1 m · RD+S3	75.1 S3 · 56.6 RD · 72.5 · 56.9	22.89 S3 · 17.26 RD · 22.09 · 17.35
V3	Villa	4,207	390.8	18.0 m · RD	59.0 RD · 69.7 · 59.1 · 72.5	17.98 RD · 21.26 · 18.00 · 22.08
V4	Villa	4,354	404.5	39.7 m · RD+S2	66.0 S2 · 64.0 · 69.7 · 64.1 RD	20.11 S2 · 19.51 · 21.26 · 19.54 RD
V5	Villa	6,081	564.9	58.7 m · RD+S2	95.2 RD arc · 36.0 RD · 42.5 arc · 87.7 · 61.5 S2	29.02 RD arc · 10.96 RD · 12.94 arc · 26.72 · 18.73 S2
V6	Villa	4,050	376.3	13.7 m · S2	45.0 S2 · 90.0 · 45.0 · 90.0	13.72 S2 · 27.43 · 13.72 · 27.43
V7	Villa	4,119	382.7	29.5 m · S1	89.8 S1 · 6.9 S1 · 88.7 · 45.3 · 40.3	27.36 S1 · 2.11 S1 · 27.03 · 13.79 · 12.28
V8	Villa	5,659	525.7	43.2 m · RD+S4	96.9 RD · 80.8 · 90.0 · 45.0 S4	29.52 RD · 24.63 · 27.43 · 13.72 S4
V9	Villa	4,050	376.3	13.7 m · S3	45.0 S3 · 90.0 · 45.0 · 90.0	13.72 S3 · 27.43 · 13.72 · 27.43
V10	Villa	4,050	376.3	13.7 m · S3	45.0 S3 · 90.0 · 45.0 · 90.0	13.72 S3 · 27.43 · 13.72 · 27.43
V11	Villa	4,050	376.2	13.7 m · S3	45.0 S3 · 90.0 · 45.0 · 90.0	13.72 S3 · 27.43 · 13.72 · 27.43
V12	Villa	4,050	376.2	13.7 m · S3	45.0 S3 · 90.0 · 45.0 · 90.0	13.72 S3 · 27.43 · 13.72 · 27.43
V13	Villa	4,050	376.2	13.7 m · S2	45.0 S2 · 90.0 · 45.0 · 90.0	13.72 S2 · 27.43 · 13.72 · 27.43
V14	Villa	4,050	376.2	13.7 m · S2	45.0 S2 · 90.0 · 45.0 · 90.0	13.72 S2 · 27.43 · 13.72 · 27.43
V15	Villa	4,050	376.3	13.7 m · S2	45.0 S2 · 90.0 · 45.0 · 90.0	13.72 S2 · 27.43 · 13.72 · 27.43
V16	Villa	4,050	376.3	41.1 m · S2+S5	90.0 S5 · 45.0 S2 · 90.0 · 45.0	27.43 S5 · 13.72 S2 · 27.43 · 13.72
V17	Villa	4,050	376.3	13.7 m · S1	45.0 S1 · 90.0 · 45.0 · 90.0	13.72 S1 · 27.43 · 13.72 · 27.43
V18	Villa	3,949	366.9	38.8 m · S1+S5	79.7 S5 · 45.0 · 90.0 · 47.6 S1 arc	24.29 S5 · 13.72 · 27.43 · 14.50 S1 arc
V19	Villa	5,793	538.2	68.0 m · RD	103.2 RD arc · 28.3 RD · 91.4 RD · 92.8	31.46 RD arc · 8.64 RD · 27.86 RD · 28.30
V20	Villa	6,414	595.8	51.8 m · RD+S4	91.2 RD · 78.7 S4 · 90.0 · 64.0	27.79 RD · 23.98 S4 · 27.43 · 19.51
V21	Villa	4,050	376.3	13.7 m · S4	45.0 S4 · 90.0 · 45.0 · 90.0	13.72 S4 · 27.43 · 13.72 · 27.43
V22	Villa	4,050	376.3	13.7 m · S4	45.0 S4 · 90.0 · 45.0 · 90.0	13.72 S4 · 27.43 · 13.72 · 27.43
V23	Villa	4,050	376.3	13.7 m · S3	45.0 S3 · 90.0 · 45.0 · 90.0	13.72 S3 · 27.43 · 13.72 · 27.43
V24	Villa	4,050	376.3	13.7 m · S3	45.0 S3 · 90.0 · 45.0 · 90.0	13.72 S3 · 27.43 · 13.72 · 27.43
V25	Villa	4,050	376.2	13.7 m · S3	45.0 S3 · 90.0 · 45.0 · 90.0	13.72 S3 · 27.43 · 13.72 · 27.43
V26	Villa	4,050	376.2	13.7 m · S3	45.0 S3 · 90.0 · 45.0 · 90.0	13.72 S3 · 27.43 · 13.72 · 27.43
V27	Villa	4,050	376.2	13.7 m · S2	45.0 S2 · 90.0 · 45.0 · 90.0	13.72 S2 · 27.43 · 13.72 · 27.43
V28	Villa	4,050	376.2	13.7 m · S2	45.0 S2 · 90.0 · 45.0 · 90.0	13.72 S2 · 27.43 · 13.72 · 27.43
V29	Villa	3,835	356.3	38.7 m · S2+S5	84.2 S2 · 42.7 S5 · 95.7 · 44.1	25.65 S2 · 13.00 S5 · 29.17 · 13.45
V30	Villa	4,592	426.6	13.8 m · S5	45.2 S5 · 107.7 · 46.7 · 95.7	13.76 S5 · 32.83 · 14.24 · 29.17
V31	Villa	5,133	476.9	13.8 m · S5	45.2 S5 · 119.7 · 46.7 · 107.7	13.76 S5 · 36.48 · 14.24 · 32.83
V32	Villa	4,050	376.3	13.7 m · S4	45.0 S4 · 90.0 · 45.0 · 90.0	13.72 S4 · 27.43 · 13.72 · 27.43
V33	Villa	4,050	376.3	13.7 m · S4	45.0 S4 · 90.0 · 45.0 · 90.0	13.72 S4 · 27.43 · 13.72 · 27.43
V34	Villa	3,616	335.9	15.2 m · RD	49.9 RD arc · 90.0 · 45.0 · 70.0	15.20 RD arc · 27.43 · 13.72 · 21.33
V35	Villa	4,050	376.3	13.7 m · S3	45.0 S3 · 90.0 · 45.0 · 90.0	13.72 S3 · 27.43 · 13.72 · 27.43
V36	Villa	4,050	376.3	13.7 m · S3	45.0 S3 · 90.0 · 45.0 · 90.0	13.72 S3 · 27.43 · 13.72 · 27.43
V37	Villa	4,181	388.5	28.8 m · S3	43.0 S3 · 31.5 S3 · 20.1 S3 · 90.5 · 9.2 · 47.5 · 10.3 · 43.8 · 29.5 · 16.5	13.11 S3 · 9.59 S3 · 6.12 S3 · 27.57 · 2.82 · 14.48 · 3.15 · 13.34 · 8.98 · 5.03
V38	Villa	4,522	420.1	20.4 m · S2	66.8 S2 · 82.1 · 47.5 · 79.8	20.35 S2 · 25.03 · 14.48 · 24.32
V39	Villa	5,870	545.4	33.3 m · RD	109.2 RD arc · 70.0 · 112.5 · 41.8	33.28 RD arc · 21.33 · 34.28 · 12.74
V40	Villa	4,050	376.3	13.7 m · S3	45.0 S3 · 90.0 · 45.0 · 90.0	13.72 S3 · 27.43 · 13.72 · 27.43
V41	Villa	6,489	602.9	25.0 m · S3	82.2 S3 arc · 84.6 · 66.8 · 88.0	25.05 S3 arc · 25.78 · 20.35 · 26.83
V42	Villa	4,911	456.2	50.4 m · RD+S4	91.6 RD arc · 28.2 · 89.8 · 73.6 S4 · 15.7	27.91 RD arc · 8.59 · 27.37 · 22.44 S4 · 4.77
V43	Villa	4,340	403.2	19.3 m · S5	63.3 S5 · 134.5 arc · 4.6 · 119.7	19.30 S5 · 40.99 arc · 1.39 · 36.48

Total 62 plots · 325,383 sq ft (30,229 m²) · 63.3% of the colony

SHEET 9 – ROADS, GARDEN MEDIANS, OPEN SPACE AND SERVICES


ROADS

Road	Runs	ROW	Cross-section	Length m	Area m²
RD	along the river-front plots, from S1 round the bend to the south end	12 m	7.5 m carriageway + 2.25 m verge with avenue trees each side	456	4,833
S1	from RD (via the bend at V5/V7) down the east boundary to S5	12 m	7.5 m carriageway + 2.25 m verge each side	70	577
S2	from RD south to the boundary (V38 stub)	12 m	3.5 m lane + 1.0 m footpath/drain each side of a 3.0 m garden median	111	1,163
S3	from RD south to the colony gate	12 m	3.5 m lane + 1.0 m footpath/drain each side of a 3.0 m garden median	155	1,258
S4	from RD south to the RD south loop	12 m	3.5 m lane + 1.0 m footpath/drain each side of a 3.0 m garden median	64	729
S5	joins S1 to S2 along V16/V18 (new)	12 m	7.5 m carriageway + 2.25 m verge each side	68	760
Access road	colony gate to the main entry	15 m	9 m carriageway + 3 m verge each side (matches the approach road)	223	3,334
Approach road	Existing main road → bridge → main entry (outside the site, as surveyed)	15 m	2 m + 1 m + 9 m carriageway + 1 m + 2 m (survey)	553	8,384
Entry splay	Joins the approach road to the access road at the main entry	—	paved	—	78
Existing road	Jalkoti ← main road → Maheshwar (survey)	5.5 m	existing carriageway	—	—

Road lengths are along the centre-line; junction areas are counted once. Every colony road is 12 m; the farthest plot (V43) is 360 m from the colony gate (BVN 38: 12 m roads up to 400 m).


ROAD CROSS-SECTIONS (metres)

12 m plain road (RD, S1, S5, gate road)

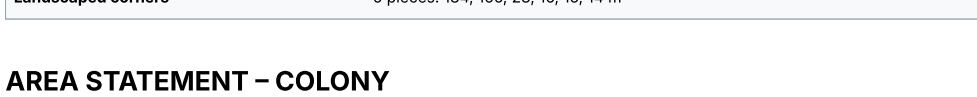


12 m garden street (S2, S3, S4)

15 m access road (through the resort)

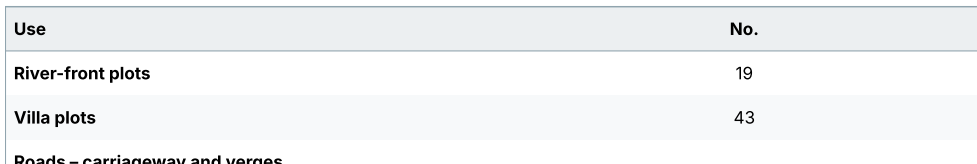

15 m approach road (survey section)

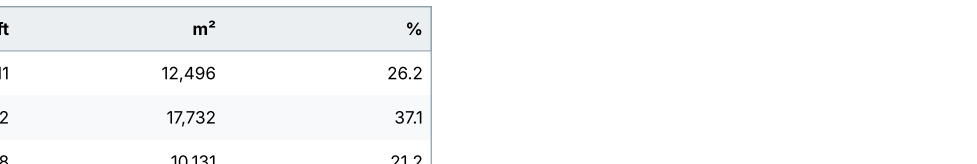

GARDEN MEDIANS (garden in the middle of the road)

Median	Width m	Length m	Area m²	Note
Median on S2	3.0	61.0	172	Stops 4 m short of junctions and before turning spaces
Median on S3	3.0	100.3	277	Stops 4 m short of junctions and before turning spaces
Median on S4	3.0	63.9	185	Stops 4 m short of junctions and before turning spaces
Total		225.2	634	Counted as road land, not open space

OPEN SPACE, WALKWAY, SERVICES AND TURNING SPACES

Item	Dimensions	Area m²	Share
Riverside garden	15 m wide (stream edge to the river-front plots); 460 m along the plots, 423 m on its centre-line	6,156	12.9%
7 ft walkway	2.13 m (7 ft) × 31.3 m, from RD between R10 and R11 to the riverside garden	66	0.1%
Services plot	24.5 × 23.2 m at the colony gate, beside the transformer	549	1.1%
STP	10.0 × 8.0 m (sewage treatment plant)	80	
Overhead tank + tubewell	7.0 × 7.0 m	49	
Waste point	5.0 × 4.0 m	20	
Turning spaces	2 × 12.0 × 11.0 m (132 m² each) at the S2 stub and the RD south end – paved, no median	264	in roads
Landscaped corners	6 pieces: 184, 166, 23, 16, 15, 14 m²	420	0.9%

AREA STATEMENT – COLONY

Use	No.	sq ft	m²	%
River-front plots	19	134,511	12,496	26.2
Villa plots	43	190,872	17,732	37.1
Roads – carriageway and verges		109,048	10,131	21.2
Garden medians (road land)		6,821	634	1.3
Riverside garden (open space)		66,261	6,156	12.9
Services plot		5,906	549	1.1
Landscaped corners		4,516	420	0.9
7 ft walkway		712	66	0.1
Total colony	62	513,947	47,747	100.0

SELLABLE 325,383 sq ft = 7.47 acres = 63.3% of the colony (62 plots)

NOTES

- Plot dimensions are in feet (1 m = 3.281 ft) on Sheets 3–8; roads, medians, garden, services and boundary in metres.
- All figures are measured from the survey drawing (Drg SU/10/01) calibrated to its surveyed areas: expect ±0.5 m.
- The approach road, bridge and existing road are traced from the same survey; the road section 2 + 1 + 9 + 1 + 2 m is the surveyor's.
- Before marking out: redraw on the CAD survey, fix the stream's high-water line on site, and check the 15 m garden width against it.
- Concept for discussion and T&CP pre-application only – not an approved layout.