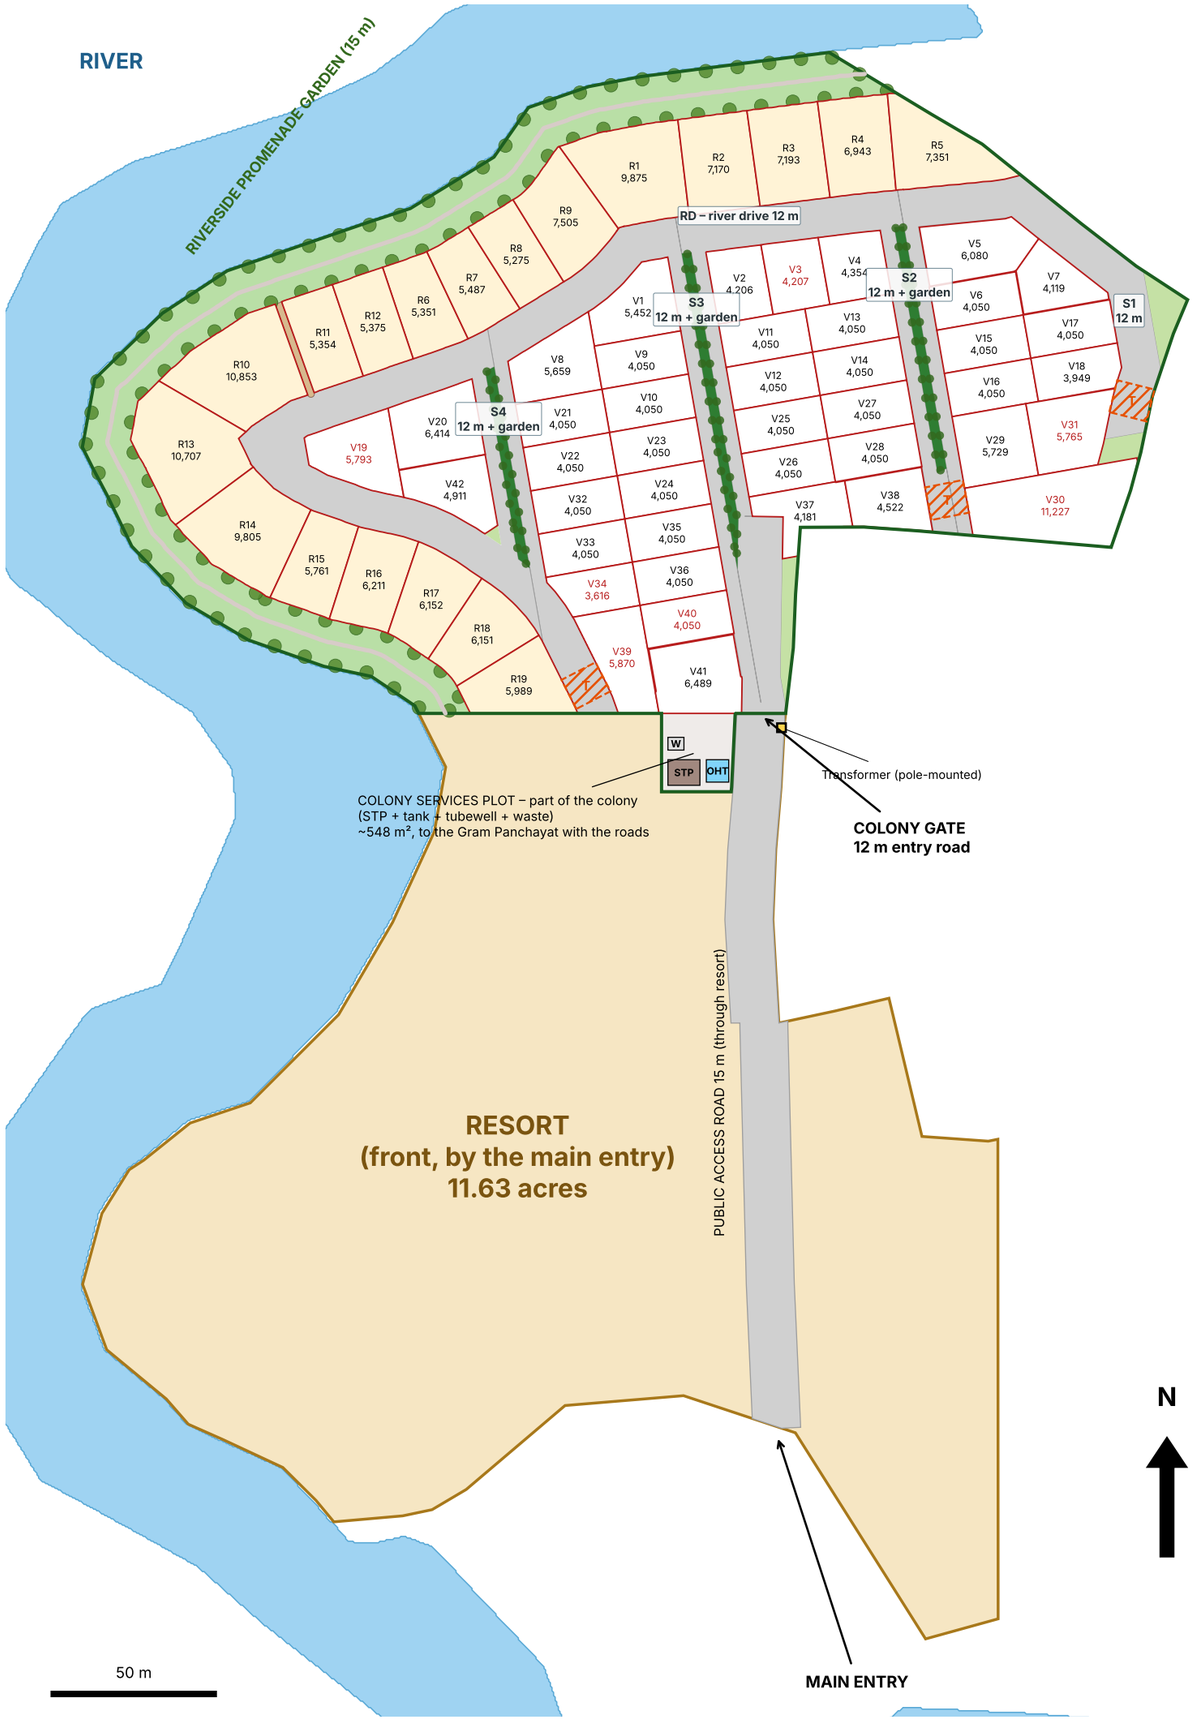


4,000 SQ FT – MAXIMUM PLOTS (ALL ROADS 12 m)

Colony at the back (river bend) + resort at the front (main entry) | Survey Drg SU/10/01, 23.325 acres

AREA STATEMENT – COLONY

Use	No.	sq ft	acre	%
River-front villa plots	19	134,507	3.09	26.2
Villa plots	42	195,696	4.49	38.1
Roads – carriageway and verges		102,492	2.35	19.9
Garden medians (part of road land)		7,469	0.17	1.5
Riverside promenade garden (15 m river setback)		66,260	1.52	12.9
Other parks that meet the open-space test		0	0.00	0.0
Landscaped corners (too small to count as park)		4,969	0.11	1.0
7 ft walkway to the promenade garden		712	0.02	0.1
Services plot – STP, tank + tubewell, waste (public utility)		5,906	0.14	1.1
Total colony		**513,943**	**11.80**	**100**

SELLABLE: 330,203 sq ft = 7.58 acres = 64.2% of colony (61 plots)

OPEN SPACE meeting the BVN test (parks): 0.0% | with promenade garden: 12.9% (minimum 10%)

GARDEN VIEW: 54 of 61 plots face the river promenade, a garden median or a park

Resort: 11.63 acres, incl. the 15 m public access road (~0.82 acre) to be dedicated as a public road

PLOT MIX

19 river-front plots 5,275–10,853 sq ft (avg 7,079), backing onto the promenade garden

42 villa plots 3,616–11,227 sq ft (avg 4,659), typical 45 × 90 ft; no clubhouse

Every plot has direct road frontage and a regular shape (plot numbers in red = no garden view)

ROADS

Public access road 15 m: main entry → through the resort → colony gate (to be a public street)

Gate entry road 12 m, plain (no plots on one side, so no median)

RD river drive 12 m, plain, avenue trees in the verges

Garden streets S2, S3, S4: 12 m = 4.5 m lane + 3 m garden median + 4.5 m lane

All roads 12 m – farthest plot 369 m from the gate (12 m allowed up to 400 m, BVN 38)

Dead ends S1, S2 and RD south end: 12 × 11 m turning space each (BVN 43: 121 m², 11 m)

DESIGN LOGIC

River-front plots back onto the riverside promenade garden – no median needed in front of them

A garden median runs only where it gives a plot its garden view – none at the gate entry, none on RD or S1

Garden medians on S2, S3 and S4 give the inner plots their garden view

Clubhouse and pool removed – they belong in the resort

Leftover strips and corners filled with plots or added to the neighbouring plot

STP, tank + tubewell and waste point in one services plot at the gate, beside the transformer (inside the colony layout)

TO CONFIRM BEFORE APPROVAL

Narmada: confirm the site is beyond 300 m of the Narmada HFL (this stream is not the Narmada)

Open space: promenade garden 12.9% (min 10%) – its long shape counts only at T&CP discretion (BVN 47(3))

Dedicate the 15 m access road as a public street before applying (BVN 2(72) + 38(6))

S1 dead end sits on a bent road – BVN 43 asks for straight cul-de-sacs; T&CP to accept

Stream: survey its highest water level; plots stay 9 m (stream) / 15 m (river) from it (BVN 50(b))

EWS/LIG by shelter fee (no land) – confirm in-lieu option under the 2014 rural rules

Scale calibrated to surveyed areas (~1:858); architect to redraw on the CAD survey

Concept for discussion only – not an approved drawing

- River-front plot
- Villa plot
- Road
- Garden median (road land)
- Riverside promenade garden
- Park (counts as open space)
- Landscaped corner
- 7 ft walkway to promenade
- T = turning space 12 × 11 m (dead end)
- STP / OHT / W = sewage plant, water tank + tubewell, waste point
- Resort