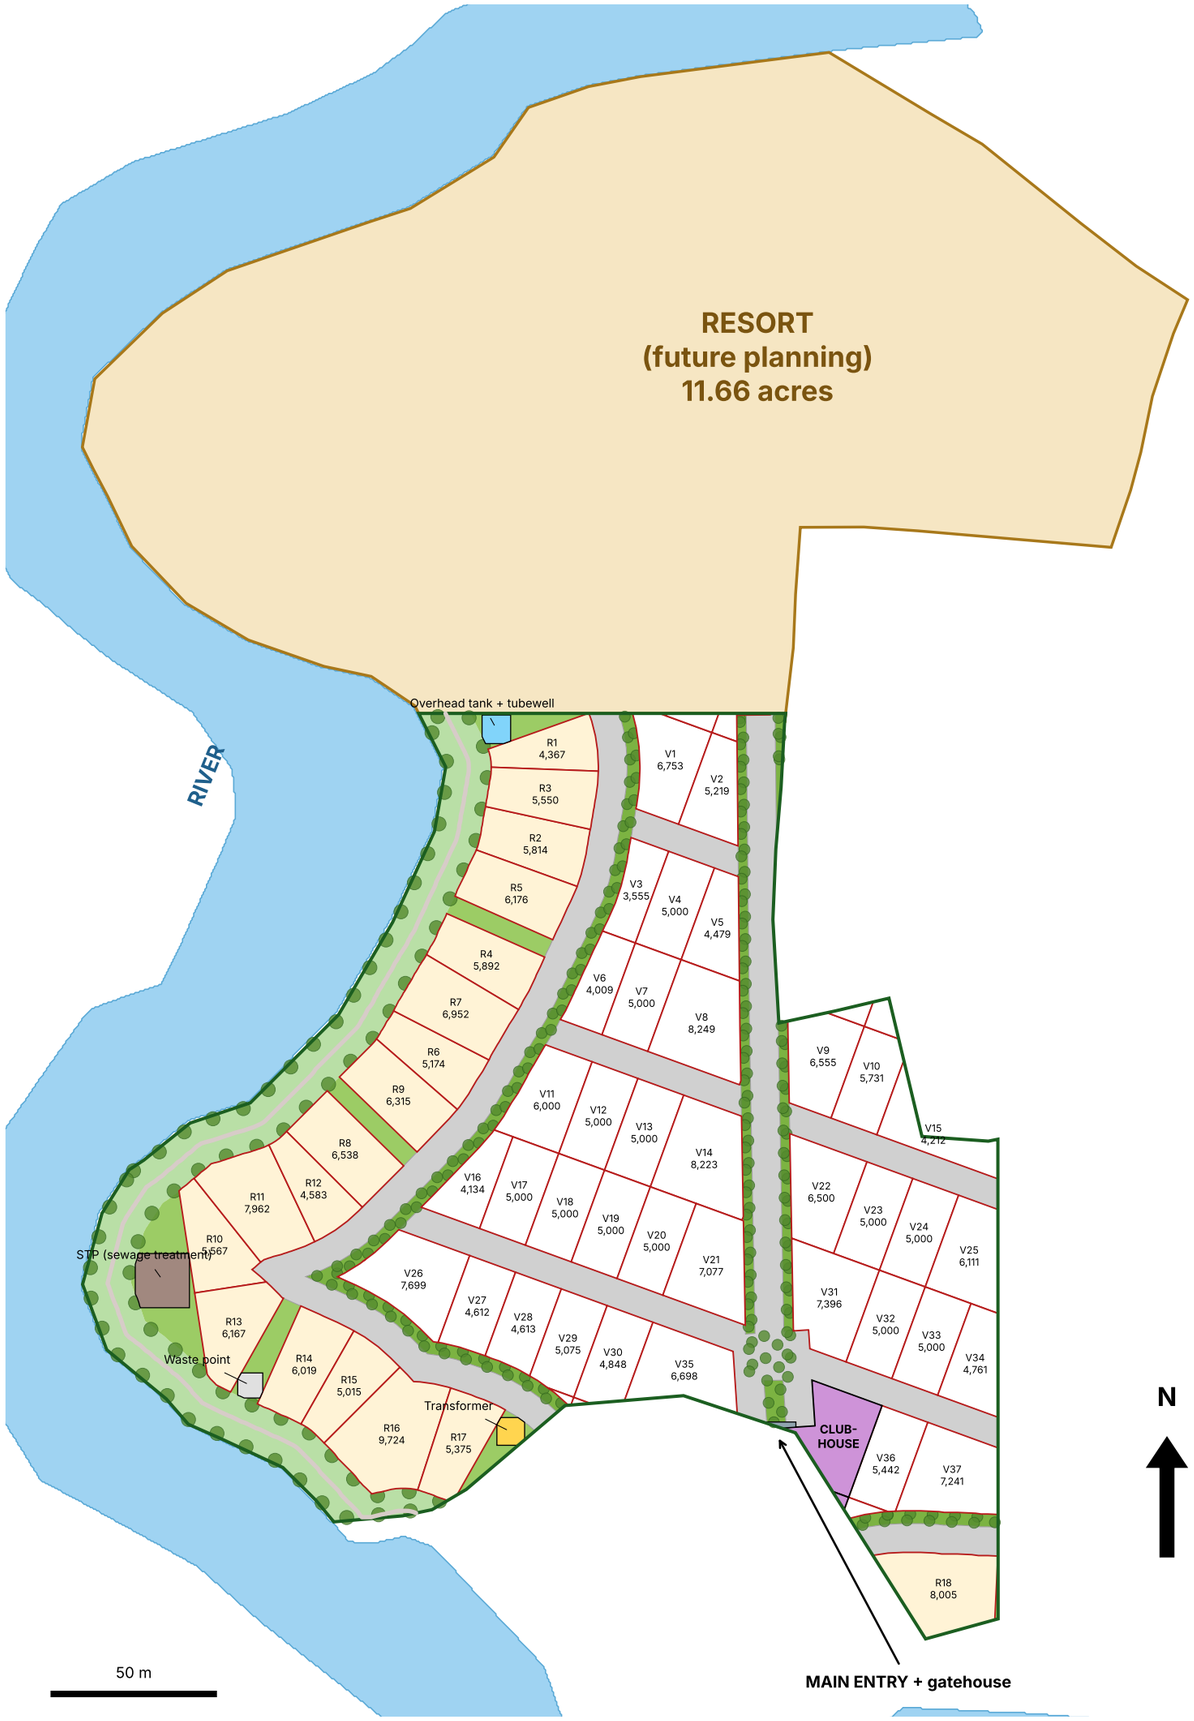


RIVER VILLAS, JALKOTI – CONCEPT MASTER PLAN

Colony (south half) + resort parcel (north half) | Survey Drg SU/10/01, total 23.325 acres

AREA STATEMENT – COLONY

Use	No.	sq ft	acre	%
River-front villa plots	18	111,195	2.55	21.7
Villa plots	37	205,192	4.71	40.0
Roads (carriageways)		91,888	2.11	17.9
Riverside promenade (15 m river buffer)		53,576	1.23	10.5
Linear gardens (drive garden, avenue verges, median)		27,723	0.64	5.4
Pocket gardens		13,798	0.32	2.7
Clubhouse / community facility		5,985	0.14	1.2
Utilities + gatehouse		5,393	0.12	1.1
Total colony		**512,668**	**11.77**	**100**

SELLABLE: 316,388 sq ft = 7.26 acres = 61.7% of colony

Open space: river promenade + gardens = 18.5% (BVN Rule 47(2) minimum 10%)

Resort parcel: 508,029 sq ft = 11.66 acres (not part of the colony sale)

PLOT MIX

18 river-front villa plots, 4,367–9,724 sq ft (avg 6,178): back onto the river promenade

37 villa plots, 3,555–8,249 sq ft (avg 5,546): most are 50 × 100 ft (5,000 sq ft)

Every plot has direct frontage on a road right-of-way (checked: 0 without frontage)

ROADS

Entry boulevard 24 m: 2 × 9 m carriageway + 6 m garden median

Resort avenue 15 m: 9 m carriageway + 3 m garden verge each side – continues to the resort

River drive 13 m: 9 m carriageway + 4 m linear garden facing the inner plots

Internal streets 9 m (BVN 2012 Rule 38: 9 m up to 250 m length)

DESIGN LOGIC

No gardens inside plots – a 5,000 sq ft plot has room for its own garden

River-front plots face the river across a continuous 15 m riverside promenade

Inner plots on the river drive and avenue face a linear garden across the road

Internal streets run at an angle that fits the site, so few plots are wasted

Odd corners become pocket gardens or utility sites; clubhouse at the entry

TO CONFIRM BEFORE APPROVAL

River identity + HFL: if this is the Narmada, the 300 m rule leaves no buildable land

T&CP to accept the 15 m river buffer as part of the 10% open space

EWS/LIG: paid as shelter fee (no land) – confirm in-lieu option under 2014 rural rules

25% of developed plots mortgaged to the Collector until completion

Planning-area status and land use (T&CP); resort needs commercial use permission

Scale calibrated to surveyed areas (~1:858); architect to redraw on CAD survey

Concept for discussion only – not an approved drawing

River-front villa plot
Villa plot
Road
Linear garden / median
Pocket garden
Riverside promenade
Clubhouse
Resort parcel