JALKOTI COLONY

Maheshwar · Khargone · Madhya Pradesh

Dimensioned layout drawings

62
plots

11.80
acres


63.3%
sellable

12 m
all roads

12.9%
open space

SHEET INDEX


01	**Location and approach**	From the Jalkoti–Maheshwar road to the colony gate	A3 · 1:4000
02	**Colony layout**	Plot numbers and areas, roads, open space, services	A3 · 1:1250
03	**Dimensioned layout**	Every plot side (ft); roads, medians, garden, boun...	A0 · 1:400
04	**Dimension sheet – north-west**	River-front plots R6–R14, the bend, S4 block	A3 · 1:500
05	**Dimension sheet – north-east**	River-front plots R1–R5, S2/S3 blocks, S1	A3 · 1:500
06	**Dimension sheet – south-west**	R15–R19, S4 and S3 blocks, RD south end	A3 · 1:500
07	**Dimension sheet – south-east**	S5 link plots, gate, services plot	A3 · 1:500
08	**Plot schedule – R1 to V12**	Area, frontage and every side of each plot	A3 · —
09	**Plot schedule – V13 to V43**	Area, frontage and every side of each plot	A3 · —
10	**Roads, medians, open space, services**	Widths, lengths, cross-sections, area statement	A3 · —

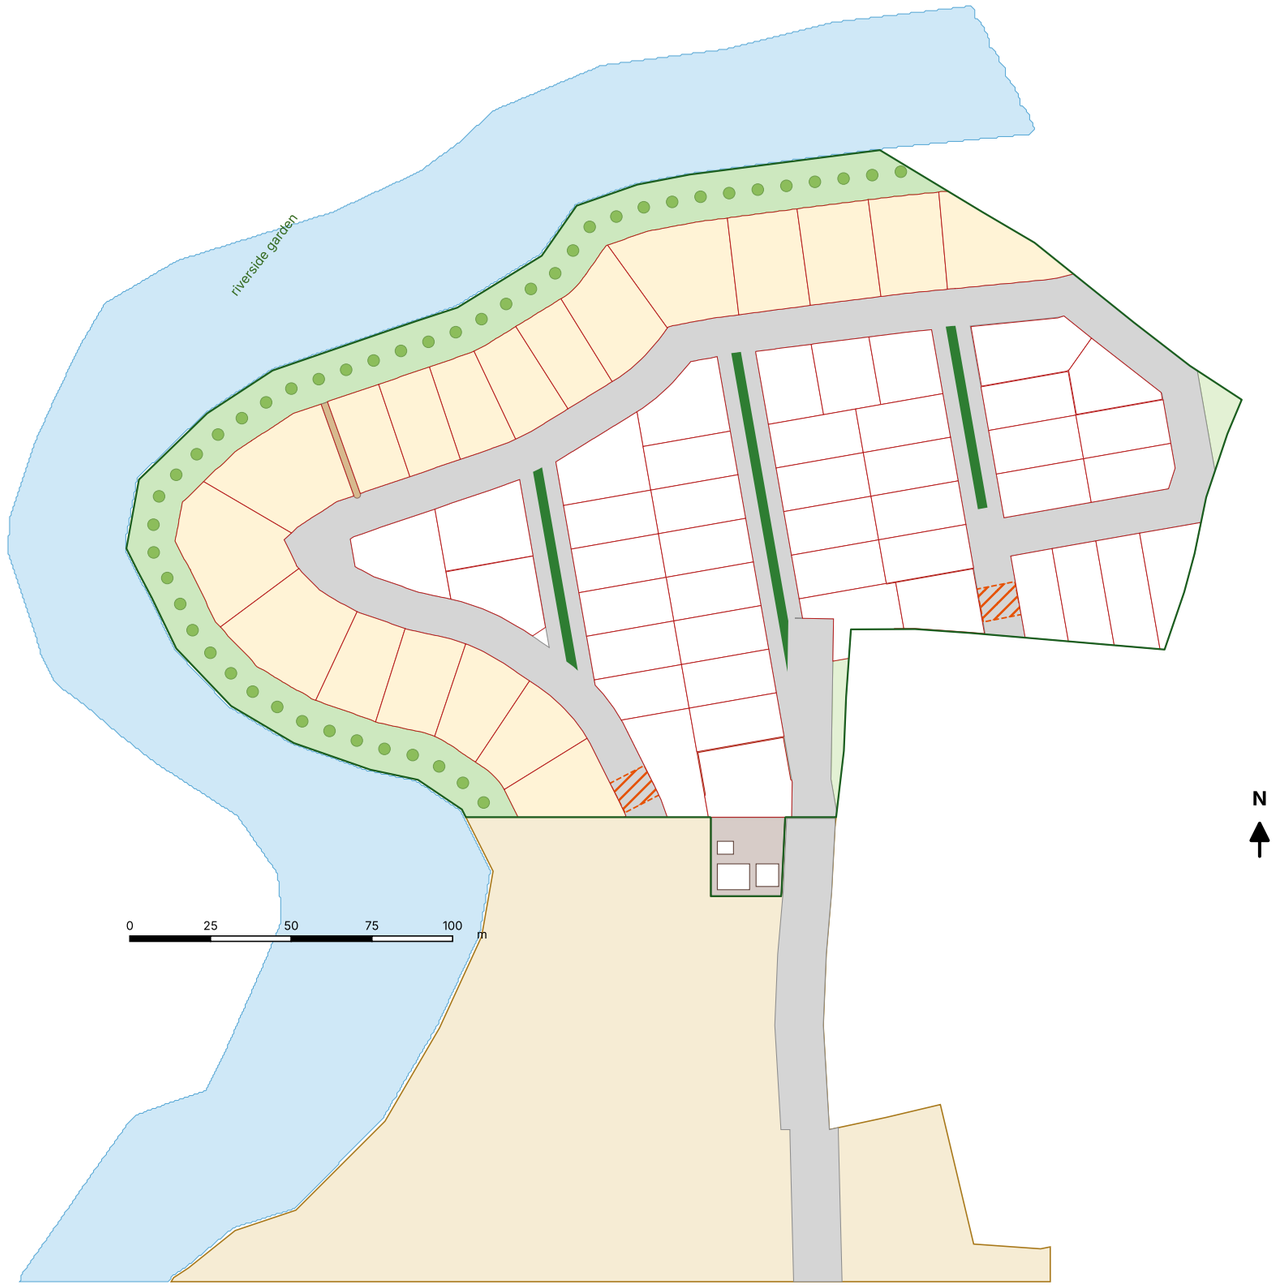

JALKOTI COLONY · MAHESHWAR Khargone, Madhya Pradesh · Survey Drg SU/10/01 · 23.325 acres	**Drawing set – cover and index** Dimensioned layout drawings for the colony	**Cover** A3 landscape	**Scale as noted** Units: m; plot sides in ft	**12 Nov 2026** Concept – not an approved drawing

01 LOCATION AND APPROACH

From the Jalkoti–Maheshwar road to the colony gate

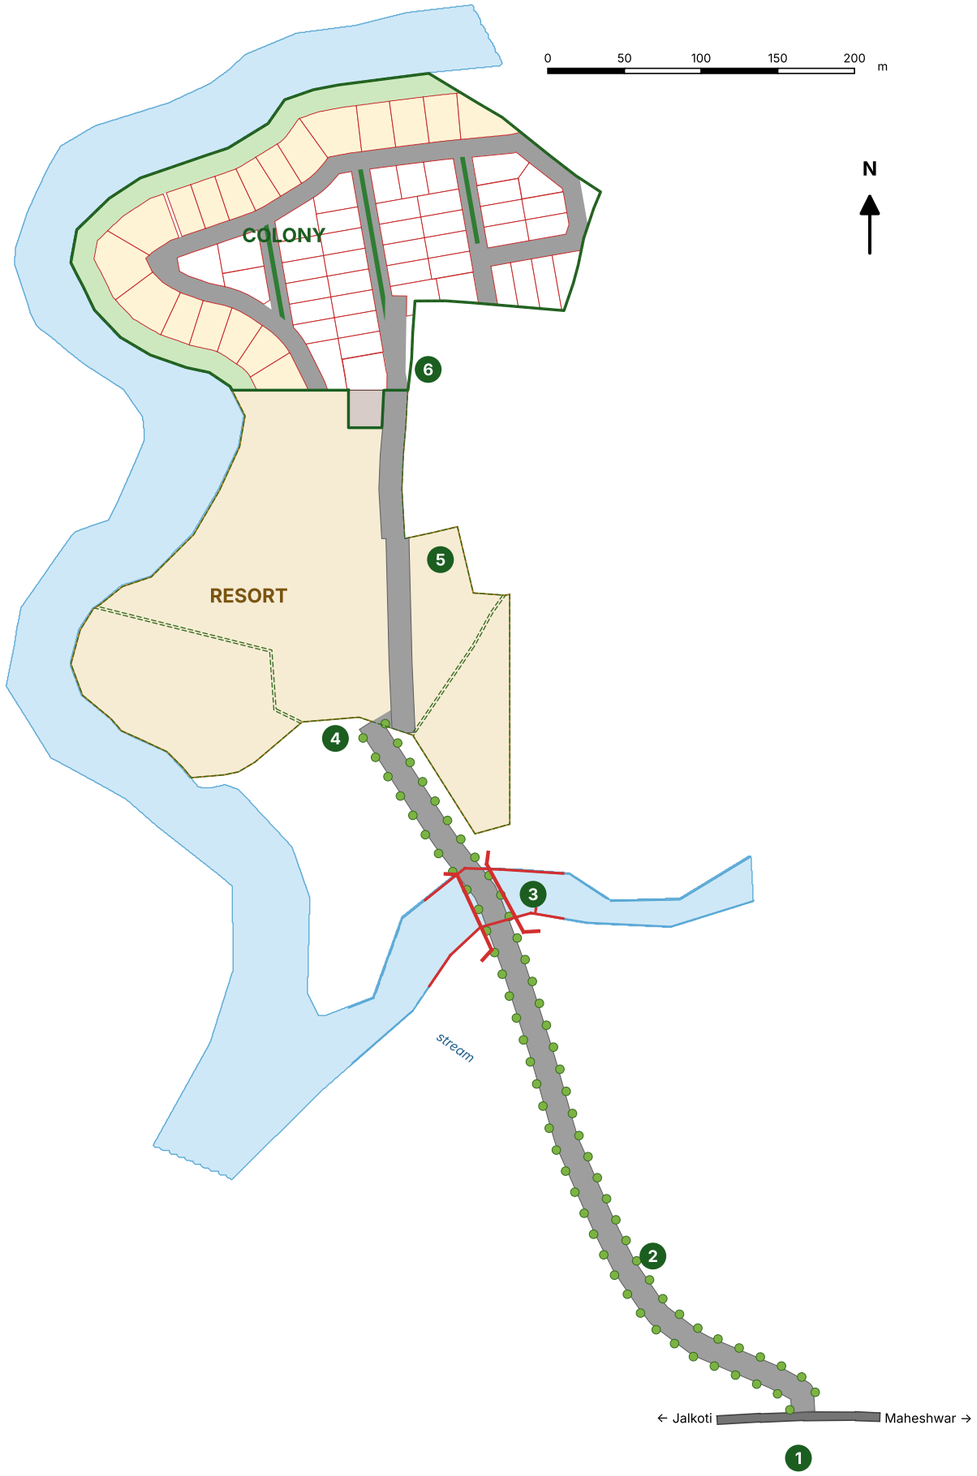

THE ROUTE FROM THE MAIN ROAD

1. **Existing Jalkoti–Maheshwar road**
   the main road, about 5.5 m wide as surveyed
2. **Approach road – about 553 m**
   15 m right of way, 9 m carriageway, avenue trees both sides
3. **Bridge over the stream**
   on the approach road, as surveyed
4. **Main entry**
   an entry splay joins the approach road to the access road
5. **Access road – about 223 m**
   15 m, through the resort land to the colony gate
6. **Colony gate**
   62 plots inside; all colony roads 12 m

Main road to the colony gate: about 800 m

Farthest plot (V43) is a further 360 m along the 12 m colony roads.

ROAD SECTIONS (metres)

Approach road (survey section)



Access road through the resort



AREAS

- Site as surveyed: 23.325 acres
- Colony: 11.80 acres (incl. services plot)
- Resort: 11.63 acres (incl. the 15 m access road)

Both the approach road and the access road should be dedicated as public roads before the colony application (BVN Rules 2(72) and 38(6)).

Approach road, bridge, existing road and mandir are traced from the survey (Drg SU/10/01, 1:1000); widths from its road lines and road section.

JALKOTI COLONY · MAHESHWAR Khargone, Madhya Pradesh · Survey Drg SU/10/01 · 23.325 acres	**Location and approach** From the Jalkoti–Maheshwar road to the colony gate	**Sheet 1 of 10** A3 landscape	**Scale 1:4000** Units: m; plot sides in ft	**12 Nov 2026** Concept – not an approved drawing

02 COLONY LAYOUT

Plot numbers and areas, roads, open space, services



AREA STATEMENT

Use	No.	sq ft	m²	%
River-front plots	19	134,511	12,496	26.2
Villa plots	43	190,872	17,732	37.1
Roads – carriageway and verges		109,048	10,131	21.2
Garden medians (road land)		6,821	634	1.3
Riverside garden (open space)		66,261	6,156	12.9
Services plot		5,906	549	1.1
Landscaped corners		4,516	420	0.9
7 ft walkway		712	66	0.1
Total colony	62	513,947	47,747	100.0

SELLABLE 325,383 sq ft

7.47 acres · 63.3% of the colony

PLOTS

- 19 river-front plots, 5,275–10,853 sq ft
- 43 villa plots, 3,616–6,489 sq ft
- Typical villa plot 45 × 90 ft (4,050 sq ft)
- Every frontage above 12 m (BVN 53)

ROADS – ALL 12 m

- RD river drive · S1 east street
- S2, S3, S4 garden streets (3 m median)
- S5 link road joins S1 to S2
- Access road 15 m · 223 m to the main entry
- Dead ends: S2 stub, RD south – turning space

- River-front plot
- Villa plot
- Road (right of way)
- Garden median (road land)
- Riverside garden (open space)
- Landscaped corner
- 7 ft walkway
- Services plot
- T = turning space 12 × 11 m
- Resort
- Colony boundary

JALKOTI COLONY · MAHESHWAR Khargone, Madhya Pradesh · Survey Drg SU/10/01 · 23.325 acres	**Colony layout** Plot numbers and areas, roads, open space, services	**Sheet 2 of 10** A3 landscape	**Scale 1:1250** Units: m; plot sides in ft	**12 Nov 2026** Concept – not an approved drawing

03 DIMENSIONED LAYOUT

Every plot side (ft); roads, medians, garden, boundary (m)



HOW TO READ

- Blue figures inside each plot: side lengths in feet
- "arc": curved side, measured along the curve
- Bold: plot number and area in sq ft
- Blue arrows across roads: right-of-way width (m)
- White text on green: median width × length (m)
- Green arrows: riverside garden width (m)
- Dark green outside the boundary: boundary lengths (m)
- T: turning space 12 × 11 m

ROADS

- RD: 12 m, about 456 m
- S1: 12 m, about 70 m
- S2: 12 m, about 111 m
- S3: 12 m, about 155 m
- S4: 12 m, about 64 m
- S5: 12 m, about 68 m
- Access road: 15 m, about 223 m

GARDEN MEDIANS

- S2: 3.0 m × 61.0 m
- S3: 3.0 m × 100.3 m
- S4: 3.0 m × 63.9 m

OPEN SPACE, SERVICES

- Riverside garden 15 m × ~460 m, 6,156 m²
- Walkway 2.13 × 31.3 m (R10/R11)
- Services plot 24.5 × 23.2 m
- STP 10 × 8 · tank 7 × 7 · waste 5 × 4 m

SETBACKS (BVN Rule 56)

- Front 3.6 m · rear 3 m · sides 3 m
- River-front: 15 m garden + 3 m rear

ACCURACY

- From the survey scan, ±0.5 m
- Redraw on CAD and verify on site

Use	No.	sq ft	m²	%
River-front plots	19	134,511	12,496	26.2
Villa plots	43	190,872	17,732	37.1
Roads – carriageway and verges		109,048	10,131	21.2
Garden medians (road land)		6,821	634	1.3
Riverside garden (open space)		66,261	6,156	12.9
Services plot		5,906	549	1.1
Landscaped corners		4,516	420	0.9
7 ft walkway		712	66	0.1
Total colony	62	513,947	47,747	100.0


SELLABLE 325,383 sq ft · 63.3%

- River-front plot
- Villa plot
- Road (right of way)
- Garden median (road land)
- Riverside garden (open space)
- Landscaped corner
- 7 ft walkway
- Services plot
- T = turning space 12 × 11 m
- Resort
- Colony boundary

JALKOTI COLONY · MAHESHWAR Khargone, Madhya Pradesh · Survey Drg SU/10/01 · 23.325 acres	**Dimensioned layout** Every plot side (ft); roads, medians, garden, boundary (m)	**Sheet 3 of 10** A0 landscape	**Scale 1:400** Units: m; plot sides in ft	**12 Nov 2026** Concept – not an approved drawing

04 DIMENSION SHEET – NORTH-WEST

River-front plots R6–R14, the bend, S4 block

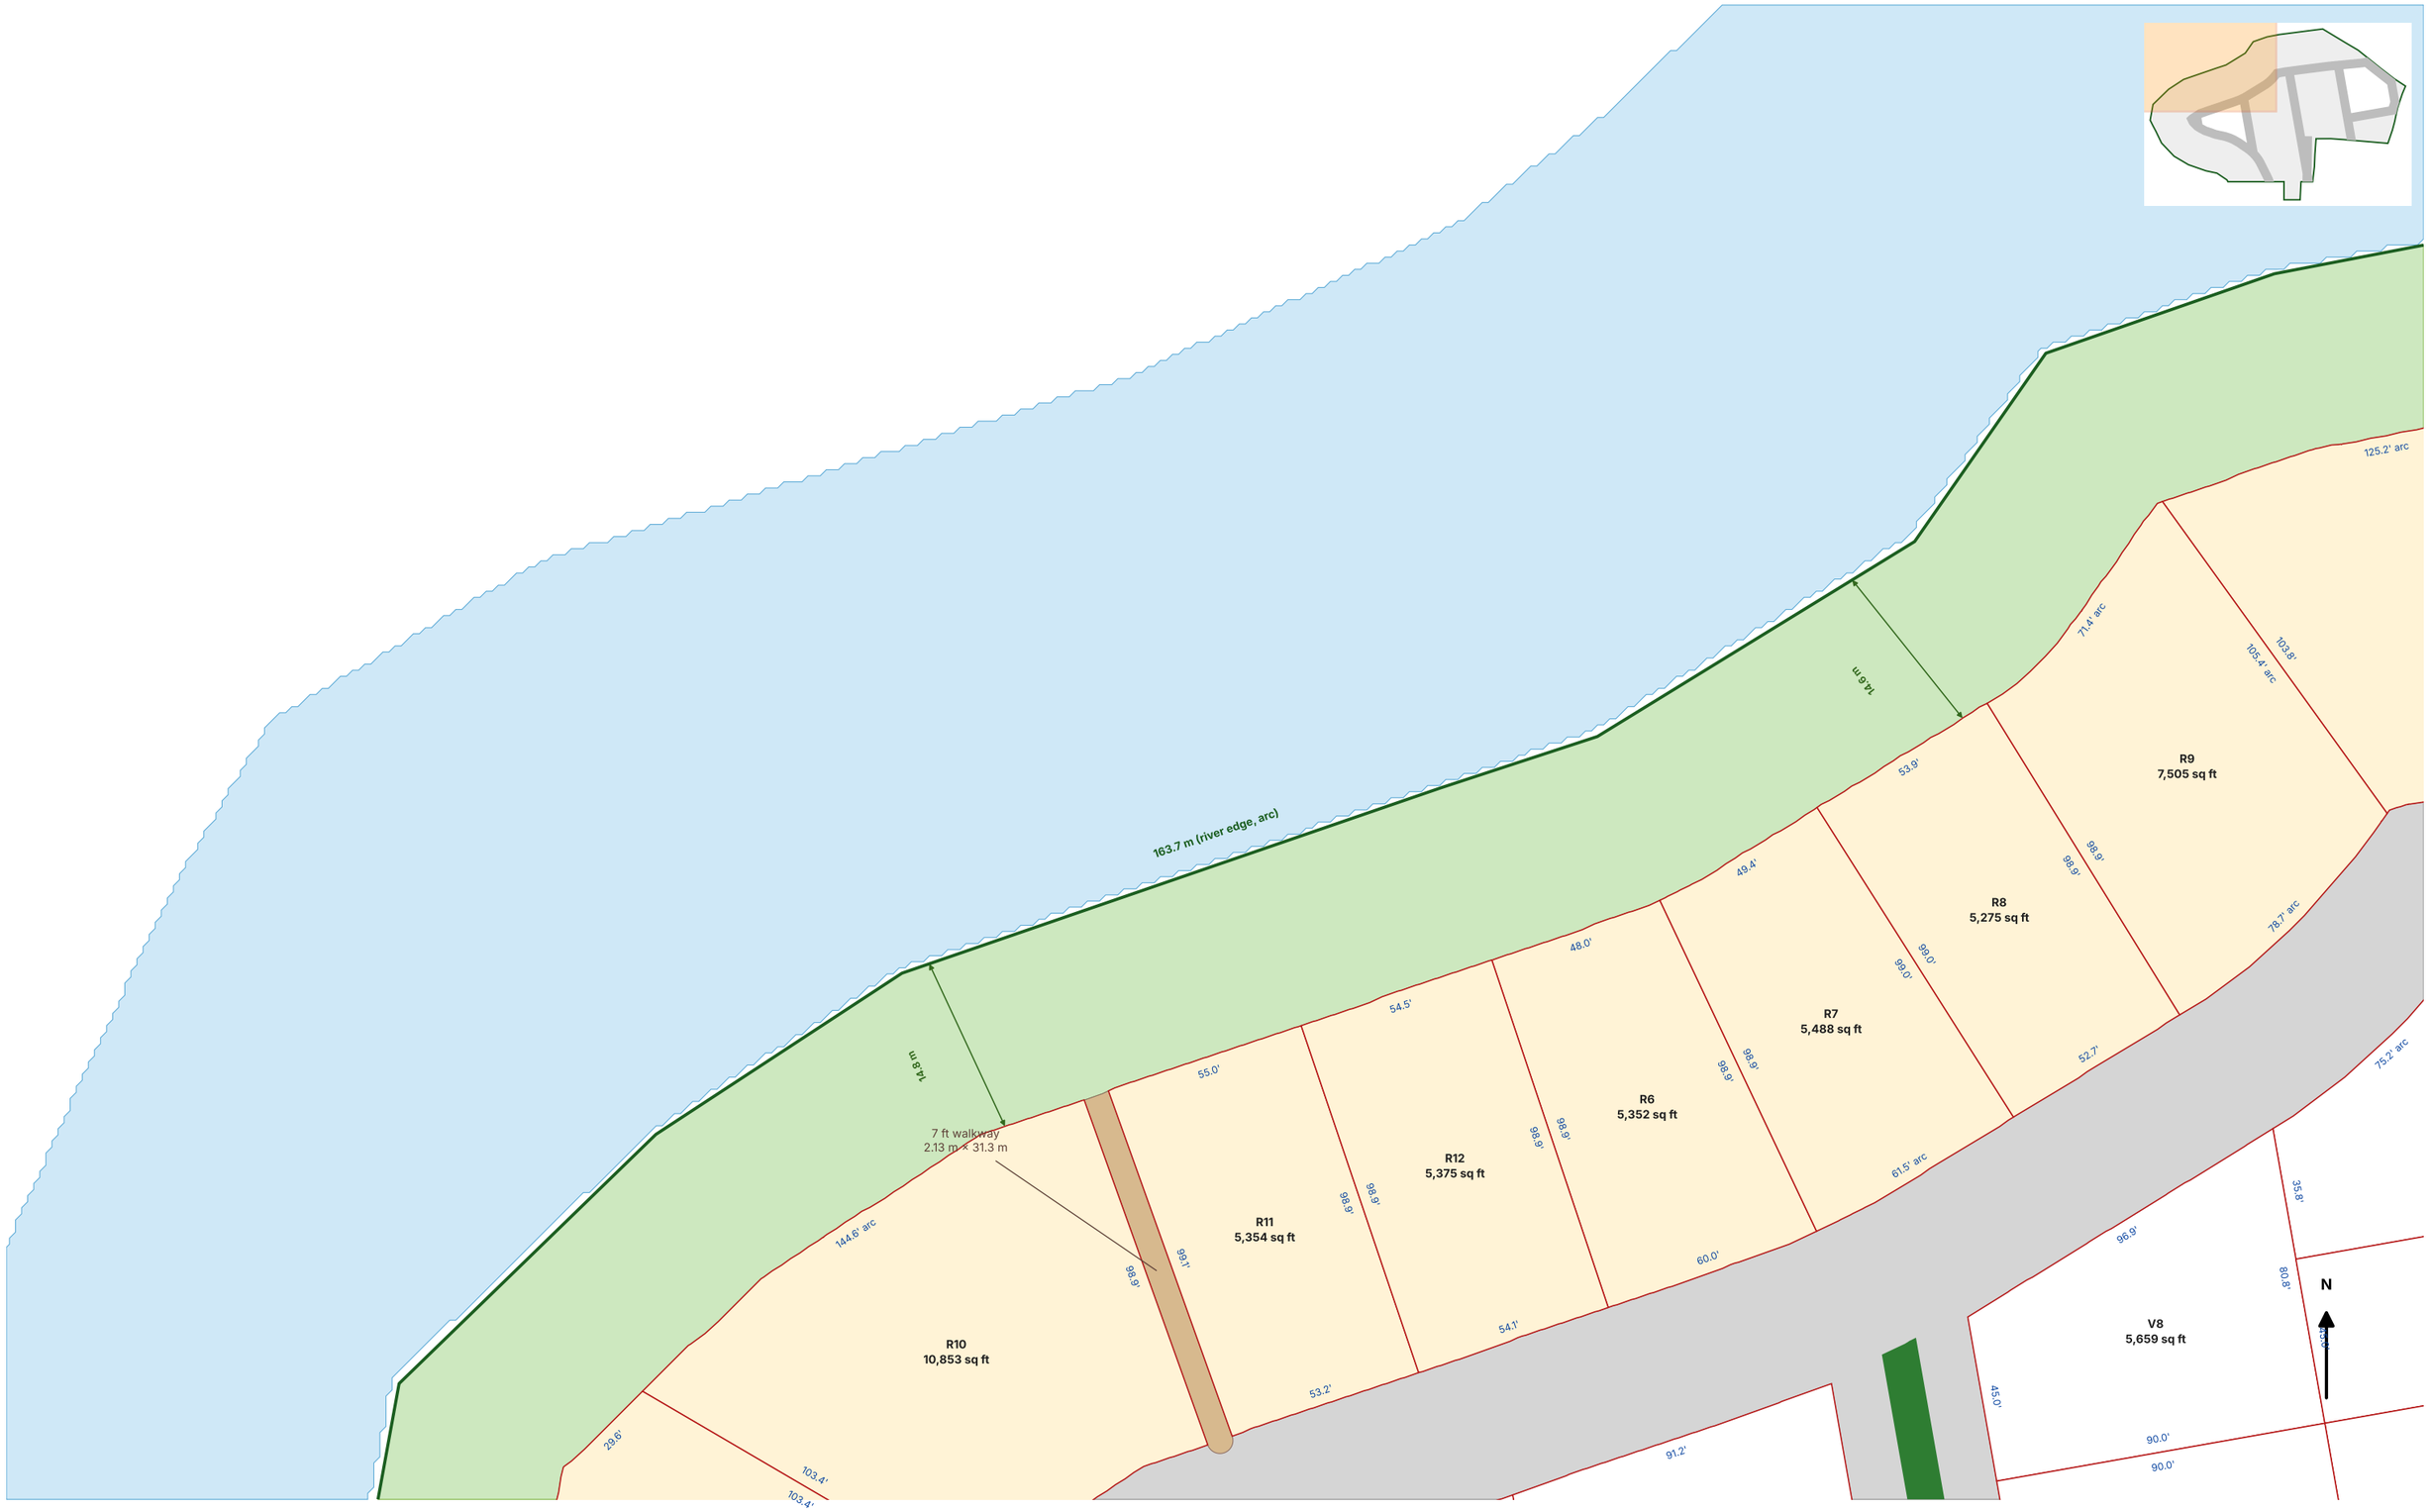

JALKOTI COLONY · MAHESHWAR Khargone, Madhya Pradesh · Survey Drg SU/10/01 · 23.325 acres	**Dimension sheet – north-west** River-front plots R6–R14, the bend, S4 block	**Sheet 4 of 10** A3 landscape	**Scale 1:500** Units: m; plot sides in ft	**12 Nov 2026** Concept – not an approved drawing

05 DIMENSION SHEET – NORTH-EAST


River-front plots R1–R5, S2/S3 blocks, S1



JALKOTI COLONY · MAHESHWAR Khargone, Madhya Pradesh · Survey Drg SU/10/01 · 23.325 acres	**Dimension sheet – north-east** River-front plots R1–R5, S2/S3 blocks, S1	**Sheet 5 of 10** A3 landscape	**Scale 1:500** Units: m; plot sides in ft	**12 Nov 2026** Concept – not an approved drawing

06 DIMENSION SHEET – SOUTH-WEST

R15–R19, S4 and S3 blocks, RD south end

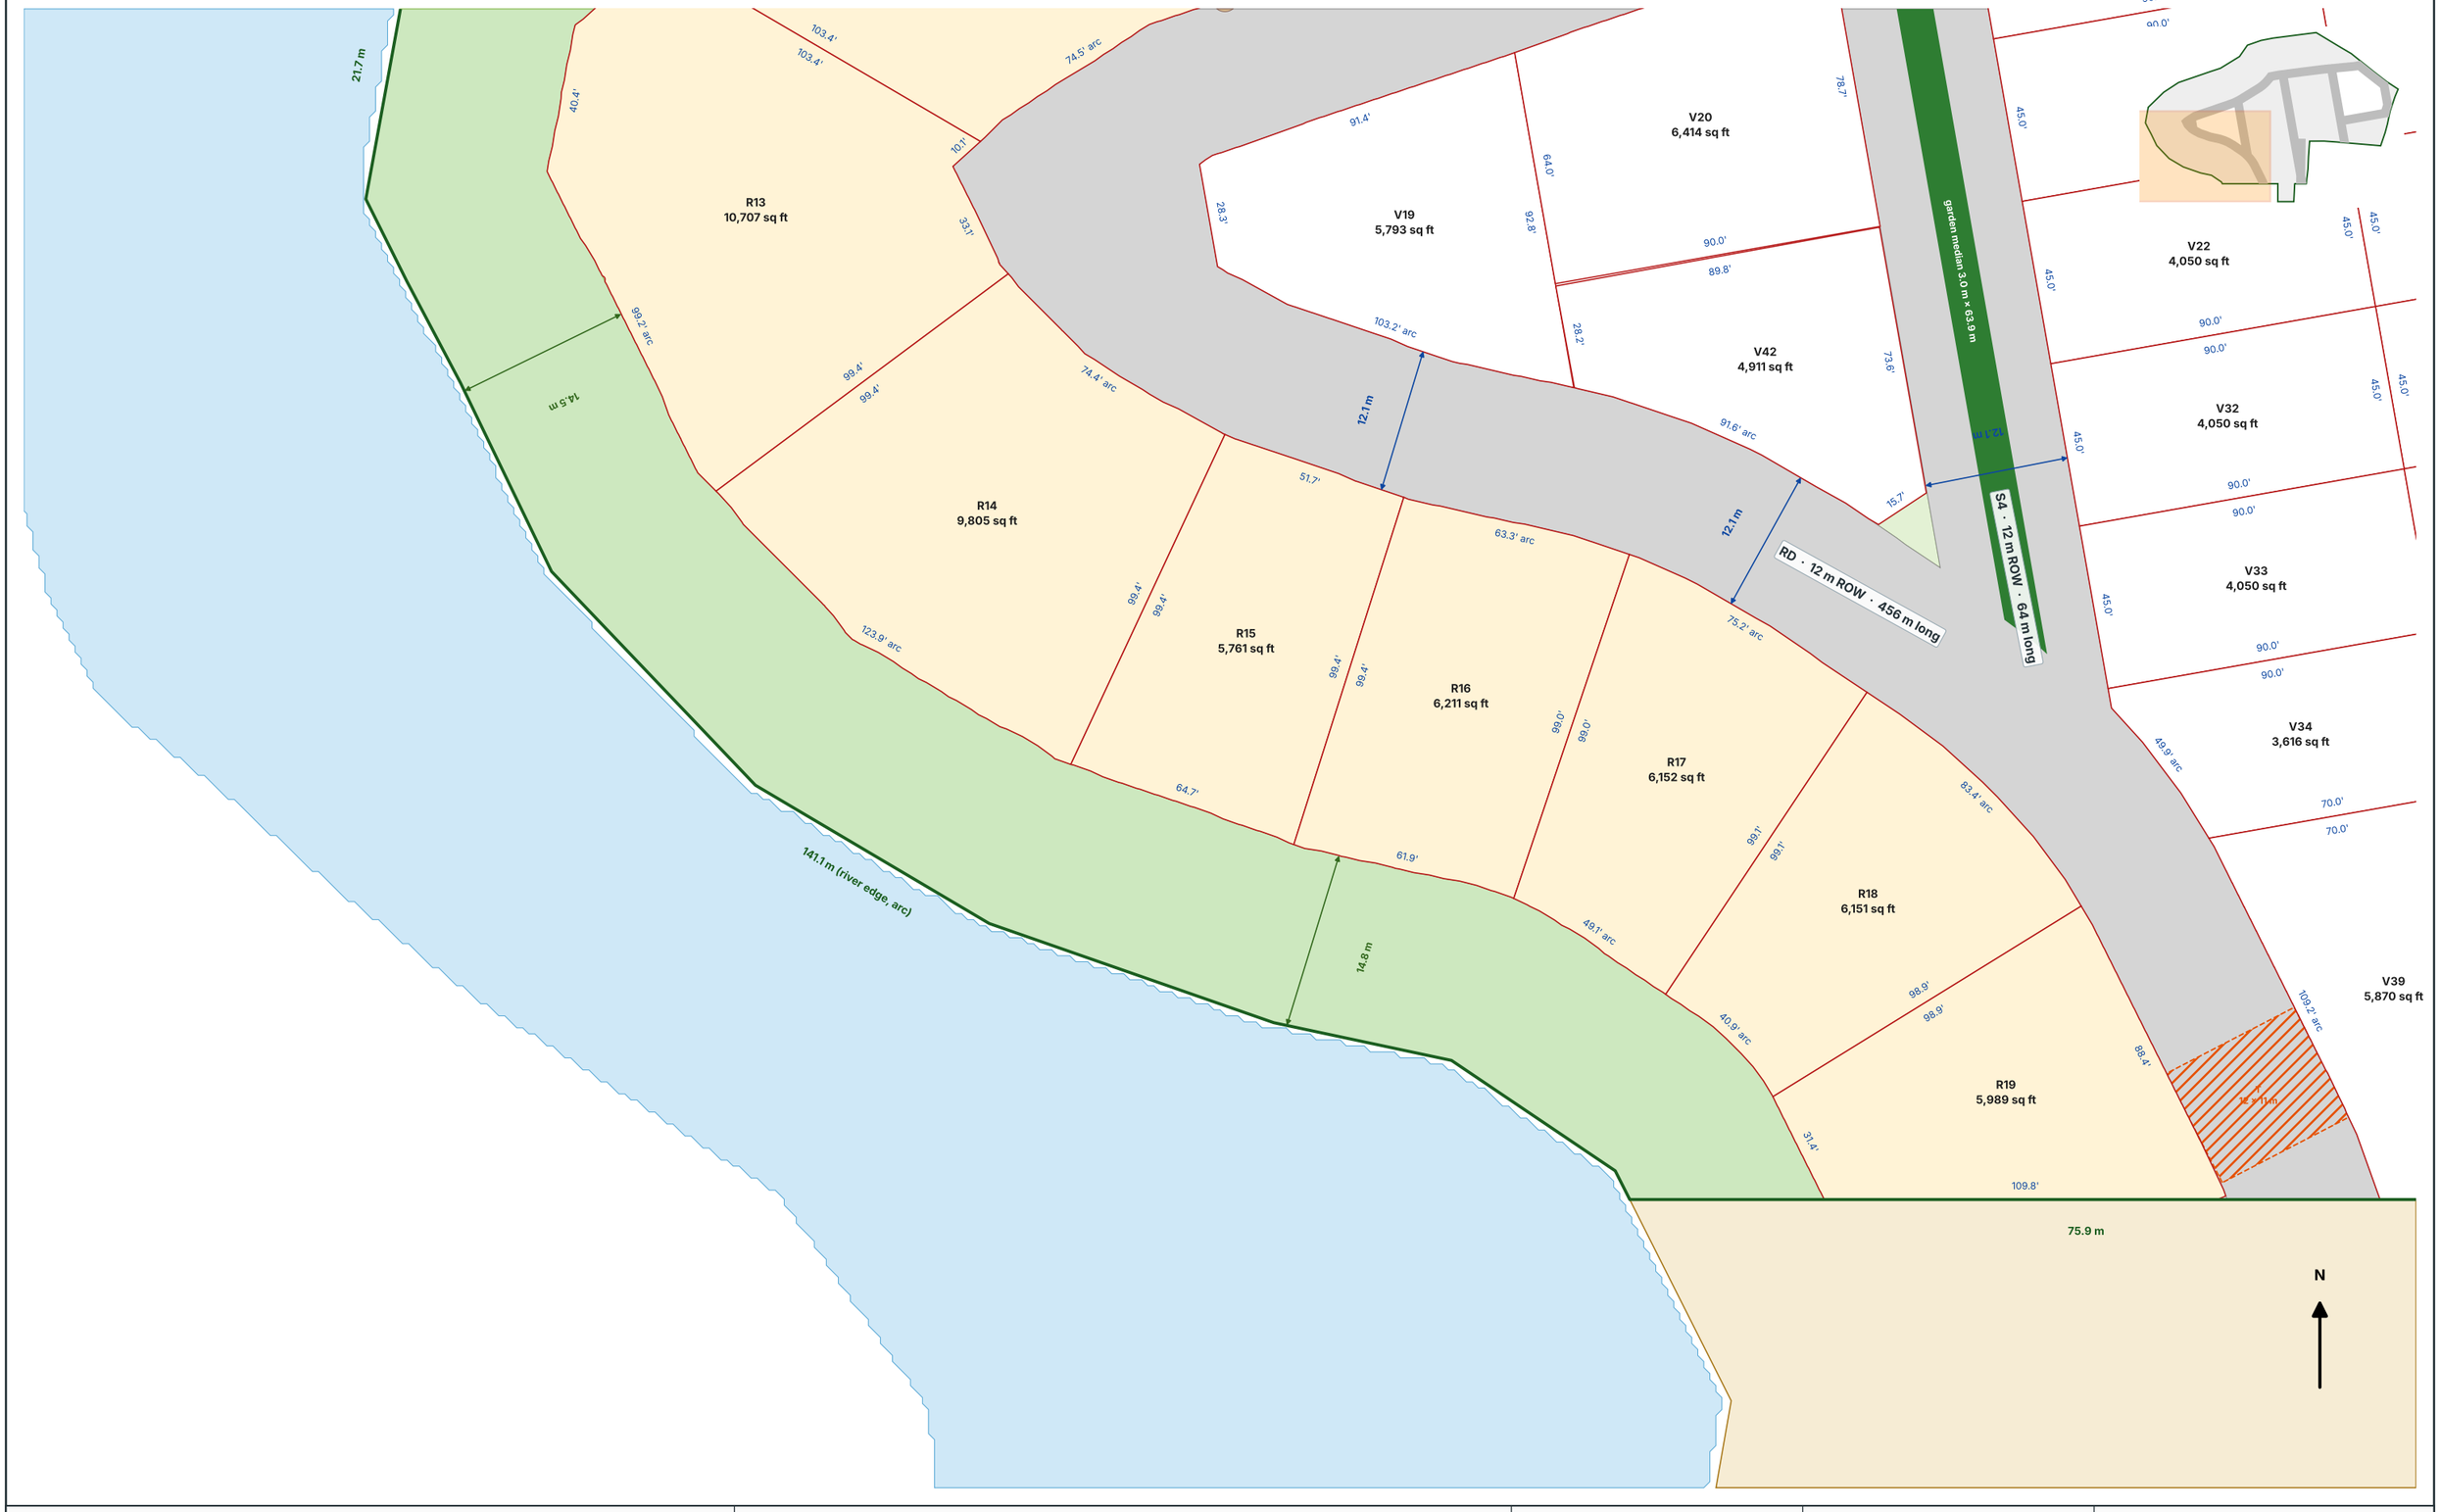

JALKOTI COLONY · MAHESHWAR Khargone, Madhya Pradesh · Survey Drg SU/10/01 · 23.325 acres	**Dimension sheet – south-west** R15–R19, S4 and S3 blocks, RD south end	**Sheet 6 of 10** A3 landscape	**Scale 1:500** Units: m; plot sides in ft	**12 Nov 2026** Concept – not an approved drawing

07 DIMENSION SHEET – SOUTH-EAST

S5 link plots, gate, services plot



JALKOTI COLONY · MAHESHWAR Khargone, Madhya Pradesh · Survey Drg SU/10/01 · 23.325 acres	**Dimension sheet – south-east** S5 link plots, gate, services plot	**Sheet 7 of 10** A3 landscape	**Scale 1:500** Units: m; plot sides in ft	**12 Nov 2026** Concept – not an approved drawing

08 PLOT SCHEDULE – R1 TO V12

Area, frontage and every side of each plot

Sides run clockwise from the front (the main road side). Road sides carry the road name; "arc" = curved side measured along the curve.

Plot	Type	sq ft	m²	Frontage	Sides in feet (clockwise from the front)	Sides in metres
R1	River-front	9,875	917.4	22.6 m · RD	74.3 RD arc · 103.8 · 125.2 arc · 98.9	22.65 RD arc · 31.64 · 38.17 arc · 30.15
R2	River-front	7,170	666.1	22.4 m · RD	73.4 RD · 98.9 · 71.5 · 98.9	22.37 RD · 30.15 · 21.78 · 30.14
R3	River-front	7,193	668.2	22.0 m · RD	72.3 RD · 98.9 · 73.1 · 99.3	22.04 RD · 30.14 · 22.27 · 30.25
R4	River-front	6,943	645.1	20.7 m · RD	68.1 RD · 99.3 · 72.3 · 99.1	20.74 RD · 30.25 · 22.03 · 30.21
R5	River-front	7,351	682.9	39.1 m · RD	128.2 RD arc · 99.1 · 9.6 · 152.2 arc	39.08 RD arc · 30.21 · 2.93 · 46.39 arc
R6	River-front	5,352	497.2	18.3 m · RD	60.0 RD · 98.9 · 48.0 · 98.9	18.28 RD · 30.15 · 14.64 · 30.14
R7	River-front	5,488	509.8	18.8 m · RD	61.5 RD arc · 98.9 · 49.4 · 99.0	18.76 RD arc · 30.14 · 15.04 · 30.18
R8	River-front	5,275	490.1	16.1 m · RD	52.7 RD · 99.0 · 53.9 · 98.9	16.07 RD · 30.18 · 16.42 · 30.14
R9	River-front	7,505	697.2	24.0 m · RD	78.7 RD arc · 98.9 · 71.4 arc · 105.4 arc	23.99 RD arc · 30.13 · 21.76 arc · 32.11 arc
R10	River-front	10,853	1,008.2	22.7 m · RD	74.5 RD arc · 103.4 · 144.6 arc · 98.9	22.71 RD arc · 31.52 · 44.09 arc · 30.16
R11	River-front	5,354	497.4	16.2 m · RD	53.2 RD · 99.1 · 55.0 · 98.9	16.22 RD · 30.19 · 16.75 · 30.15
R12	River-front	5,375	499.4	16.5 m · RD	54.1 RD · 98.9 · 54.5 · 98.9	16.50 RD · 30.15 · 16.60 · 30.15
R13	River-front	10,707	994.7	13.2 m · RD	33.1 RD · 99.4 · 99.2 arc · 40.4 · 29.6 · 103.4 · 10.1 RD	10.09 RD · 30.29 · 30.24 arc · 12.32 · 9.03 · 31.52 · 3.09 RD
R14	River-front	9,805	910.9	22.7 m · RD	74.4 RD arc · 99.4 · 123.9 arc · 99.4	22.67 RD arc · 30.29 · 37.76 arc · 30.29
R15	River-front	5,761	535.2	15.8 m · RD	51.7 RD · 99.4 · 64.7 · 99.4	15.77 RD · 30.29 · 19.71 · 30.29
R16	River-front	6,211	577.0	19.3 m · RD	63.3 RD arc · 99.0 · 61.9 · 99.4	19.31 RD arc · 30.18 · 18.86 · 30.29
R17	River-front	6,152	571.5	22.9 m · RD	75.2 RD arc · 99.1 · 49.1 arc · 99.0	22.91 RD arc · 30.19 · 14.97 arc · 30.18
R18	River-front	6,151	571.4	25.4 m · RD	83.4 RD arc · 98.9 · 40.9 arc · 99.1	25.42 RD arc · 30.15 · 12.48 arc · 30.19
R19	River-front	5,989	556.4	27.0 m · RD	88.4 RD · 109.8 · 31.4 · 98.9	26.96 RD · 33.46 · 9.56 · 30.15
V1	Villa	5,452	506.5	54.6 m · RD+S3	76.8 S3 · 90.0 · 35.8 · 75.2 RD arc · 27.3 RD	23.41 S3 · 27.43 · 10.91 · 22.91 RD arc · 8.32 RD
V2	Villa	4,206	390.8	40.1 m · RD+S3	75.1 S3 · 56.6 RD · 72.5 · 56.9	22.89 S3 · 17.26 RD · 22.09 · 17.35
V3	Villa	4,207	390.8	18.0 m · RD	59.0 RD · 69.7 · 59.1 · 72.5	17.98 RD · 21.26 · 18.00 · 22.08
V4	Villa	4,354	404.5	39.7 m · RD+S2	66.0 S2 · 64.0 · 69.7 · 64.1 RD	20.11 S2 · 19.51 · 21.26 · 19.54 RD
V5	Villa	6,081	564.9	58.7 m · RD+S2	95.2 RD arc · 36.0 RD · 42.5 arc · 87.7 · 61.5 S2	29.02 RD arc · 10.96 RD · 12.94 arc · 26.72 · 18.73 S2
V6	Villa	4,050	376.3	13.7 m · S2	45.0 S2 · 90.0 · 45.0 · 90.0	13.72 S2 · 27.43 · 13.72 · 27.43
V7	Villa	4,119	382.7	29.5 m · S1	89.8 S1 · 6.9 S1 · 88.7 · 45.3 · 40.3	27.36 S1 · 2.11 S1 · 27.03 · 13.79 · 12.28
V8	Villa	5,659	525.7	43.2 m · RD+S4	96.9 RD · 80.8 · 90.0 · 45.0 S4	29.52 RD · 24.63 · 27.43 · 13.72 S4
V9	Villa	4,050	376.3	13.7 m · S3	45.0 S3 · 90.0 · 45.0 · 90.0	13.72 S3 · 27.43 · 13.72 · 27.43
V10	Villa	4,050	376.3	13.7 m · S3	45.0 S3 · 90.0 · 45.0 · 90.0	13.72 S3 · 27.43 · 13.72 · 27.43
V11	Villa	4,050	376.2	13.7 m · S3	45.0 S3 · 90.0 · 45.0 · 90.0	13.72 S3 · 27.43 · 13.72 · 27.43
V12	Villa	4,050	376.2	13.7 m · S3	45.0 S3 · 90.0 · 45.0 · 90.0	13.72 S3 · 27.43 · 13.72 · 27.43

Measured from the calibrated survey scan (±0.5 m) – redraw on the CAD survey and verify on site before marking out.

09 PLOT SCHEDULE – V13 TO V43

Area, frontage and every side of each plot

Sides run clockwise from the front (the main road side). Road sides carry the road name; "arc" = curved side measured along the curve.

Plot	Type	sq ft	m²	Frontage	Sides in feet (clockwise from the front)	Sides in metres
V13	Villa	4,050	376.2	13.7 m · S2	45.0 S2 · 90.0 · 45.0 · 90.0	13.72 S2 · 27.43 · 13.72 · 27.43
V14	Villa	4,050	376.2	13.7 m · S2	45.0 S2 · 90.0 · 45.0 · 90.0	13.72 S2 · 27.43 · 13.72 · 27.43
V15	Villa	4,050	376.3	13.7 m · S2	45.0 S2 · 90.0 · 45.0 · 90.0	13.72 S2 · 27.43 · 13.72 · 27.43
V16	Villa	4,050	376.3	41.1 m · S2+S5	90.0 S5 · 45.0 S2 · 90.0 · 45.0	27.43 S5 · 13.72 S2 · 27.43 · 13.72
V17	Villa	4,050	376.3	13.7 m · S1	45.0 S1 · 90.0 · 45.0 · 90.0	13.72 S1 · 27.43 · 13.72 · 27.43
V18	Villa	3,949	366.9	38.8 m · S1+S5	79.7 S5 · 45.0 · 90.0 · 47.6 S1 arc	24.29 S5 · 13.72 · 27.43 · 14.50 S1 arc
V19	Villa	5,793	538.2	68.0 m · RD	103.2 RD arc · 28.3 RD · 91.4 RD · 92.8	31.46 RD arc · 8.64 RD · 27.86 RD · 28.30
V20	Villa	6,414	595.8	51.8 m · RD+S4	91.2 RD · 78.7 S4 · 90.0 · 64.0	27.79 RD · 23.98 S4 · 27.43 · 19.51
V21	Villa	4,050	376.3	13.7 m · S4	45.0 S4 · 90.0 · 45.0 · 90.0	13.72 S4 · 27.43 · 13.72 · 27.43
V22	Villa	4,050	376.3	13.7 m · S4	45.0 S4 · 90.0 · 45.0 · 90.0	13.72 S4 · 27.43 · 13.72 · 27.43
V23	Villa	4,050	376.3	13.7 m · S3	45.0 S3 · 90.0 · 45.0 · 90.0	13.72 S3 · 27.43 · 13.72 · 27.43
V24	Villa	4,050	376.3	13.7 m · S3	45.0 S3 · 90.0 · 45.0 · 90.0	13.72 S3 · 27.43 · 13.72 · 27.43
V25	Villa	4,050	376.2	13.7 m · S3	45.0 S3 · 90.0 · 45.0 · 90.0	13.72 S3 · 27.43 · 13.72 · 27.43
V26	Villa	4,050	376.2	13.7 m · S3	45.0 S3 · 90.0 · 45.0 · 90.0	13.72 S3 · 27.43 · 13.72 · 27.43
V27	Villa	4,050	376.2	13.7 m · S2	45.0 S2 · 90.0 · 45.0 · 90.0	13.72 S2 · 27.43 · 13.72 · 27.43
V28	Villa	4,050	376.2	13.7 m · S2	45.0 S2 · 90.0 · 45.0 · 90.0	13.72 S2 · 27.43 · 13.72 · 27.43
V29	Villa	3,835	356.3	38.7 m · S2+S5	84.2 S2 · 42.7 S5 · 95.7 · 44.1	25.65 S2 · 13.00 S5 · 29.17 · 13.45
V30	Villa	4,592	426.6	13.8 m · S5	45.2 S5 · 107.7 · 46.7 · 95.7	13.76 S5 · 32.83 · 14.24 · 29.17
V31	Villa	5,133	476.9	13.8 m · S5	45.2 S5 · 119.7 · 46.7 · 107.7	13.76 S5 · 36.48 · 14.24 · 32.83
V32	Villa	4,050	376.3	13.7 m · S4	45.0 S4 · 90.0 · 45.0 · 90.0	13.72 S4 · 27.43 · 13.72 · 27.43
V33	Villa	4,050	376.3	13.7 m · S4	45.0 S4 · 90.0 · 45.0 · 90.0	13.72 S4 · 27.43 · 13.72 · 27.43
V34	Villa	3,616	335.9	15.2 m · RD	49.9 RD arc · 90.0 · 45.0 · 70.0	15.20 RD arc · 27.43 · 13.72 · 21.33
V35	Villa	4,050	376.3	13.7 m · S3	45.0 S3 · 90.0 · 45.0 · 90.0	13.72 S3 · 27.43 · 13.72 · 27.43
V36	Villa	4,050	376.3	13.7 m · S3	45.0 S3 · 90.0 · 45.0 · 90.0	13.72 S3 · 27.43 · 13.72 · 27.43
V37	Villa	4,181	388.5	28.8 m · S3	43.0 S3 · 31.5 S3 · 20.1 S3 · 90.5 · 9.2 · 47.5 · 10.3 · 43.8 · 29.5 · 16.5	13.11 S3 · 9.59 S3 · 6.12 S3 · 27.57 · 2.82 · 14.48 · 3.15 · 13.34 · 8.98 · 5.03
V38	Villa	4,522	420.1	20.4 m · S2	66.8 S2 · 82.1 · 47.5 · 79.8	20.35 S2 · 25.03 · 14.48 · 24.32
V39	Villa	5,870	545.4	33.3 m · RD	109.2 RD arc · 70.0 · 112.5 · 41.8	33.28 RD arc · 21.33 · 34.28 · 12.74
V40	Villa	4,050	376.3	13.7 m · S3	45.0 S3 · 90.0 · 45.0 · 90.0	13.72 S3 · 27.43 · 13.72 · 27.43
V41	Villa	6,489	602.9	25.0 m · S3	82.2 S3 arc · 84.6 · 66.8 · 88.0	25.05 S3 arc · 25.78 · 20.35 · 26.83
V42	Villa	4,911	456.2	50.4 m · RD+S4	91.6 RD arc · 28.2 · 89.8 · 73.6 S4 · 15.7	27.91 RD arc · 8.59 · 27.37 · 22.44 S4 · 4.77
V43	Villa	4,340	403.2	19.3 m · S5	63.3 S5 · 134.5 arc · 4.6 · 119.7	19.30 S5 · 40.99 arc · 1.39 · 36.48

Total 62 plots · 325,383 sq ft (30,229 m²) · 63.3% of the colony

Measured from the calibrated survey scan (±0.5 m) – redraw on the CAD survey and verify on site before marking out.

JALKOTI COLONY · MAHESHWAR Khargone, Madhya Pradesh · Survey Drg SU/10/01 · 23.325 acres	**Plot schedule – V13 to V43** Area, frontage and every side of each plot	**Sheet 9 of 10** A3 landscape	**Scale —** Units: m; plot sides in ft	**12 Nov 2026** Concept – not an approved drawing

10 ROADS, MEDIANS, OPEN SPACE, SERVICES

Widths, lengths, cross-sections, area statement

ROADS

Road	Runs	ROW	Length m	Area m²
RD	along the river-front plots, from S1 round the bend to the south end	12 m	456	4,833
S1	from RD (via the bend at V5/V7) down the east boundary to S5	12 m	70	577
S2	from RD south to the boundary (V38 stub)	12 m	111	1,163
S3	from RD south to the colony gate	12 m	155	1,258
S4	from RD south to the RD south loop	12 m	64	729
S5	joins S1 to S2 along V16/V18 (new)	12 m	68	760
Access road	colony gate to the main entry	15 m	223	3,334
Approach road	Main road → bridge → main entry (survey)	15 m	553	8,384
Entry splay	Approach road to access road at the main entry	—	—	78
Existing road	Jalkoti ← main road → Maheshwar (survey)	5.5 m	—	—


Lengths along the centre-line, junctions counted once. Farthest plot (V43) is 360 m from the colony gate (BVN 38: 12 m roads up to 400 m).

ROAD CROSS-SECTIONS (metres)

12 m plain road – RD, S1, S5, gate road



12 m garden street – S2, S3, S4

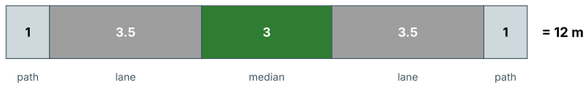

15 m access road – through the resort



15 m approach road – survey section



GARDEN MEDIANS

Median	Width m	Length m	Area m²	Note
Median on S2	3.0	61.0	172	stops 4 m short of junctions
Median on S3	3.0	100.3	277	stops 4 m short of junctions
Median on S4	3.0	63.9	185	stops 4 m short of junctions
Total		225.2	634	road land, not open space

OPEN SPACE, WALKWAY, SERVICES

Item	Dimensions	Area m²
Riverside garden	15 m wide · 460 m along the plots	6,156
7 ft walkway	2.13 × 31.3 m, R10/R11 to the garden	66
Services plot	24.5 × 23.2 m at the colony gate	549
STP	10.0 × 8.0 m	80
Tank + tubewell	7.0 × 7.0 m	49
Waste point	5.0 × 4.0 m	20
Turning spaces	2 × 12.0 × 11.0 m (in the roads)	264
Landscaped corners	6 pieces	420

AREA STATEMENT – COLONY

Use	No.	sq ft	m²	%
River-front plots	19	134,511	12,496	26.2
Villa plots	43	190,872	17,732	37.1
Roads – carriageway and verges		109,048	10,131	21.2
Garden medians (road land)		6,821	634	1.3
Riverside garden (open space)		66,261	6,156	12.9
Services plot		5,906	549	1.1
Landscaped corners		4,516	420	0.9
7 ft walkway		712	66	0.1
Total colony	62	513,947	47,747	100.0

SELLABLE 325,383 sq ft = 7.47 acres = 63.3%

Plot sides in feet (1 m = 3.281 ft); everything else in metres.
Measured from the survey scan (±0.5 m). Concept for discussion and T&CP pre-application only.

JALKOTI COLONY · MAHESHWAR Khargone, Madhya Pradesh · Survey Drg SU/10/01 · 23.325 acres	**Roads, medians, open space, services** Widths, lengths, cross-sections, area statement	**Sheet 10 of 10** A3 landscape	**Scale —** Units: m; plot sides in ft	**12 Nov 2026** Concept – not an approved drawing