JALKOTI COLONY

Maheshwar · Khargone · Madhya Pradesh

Dimensioned layout drawings · portrait set



62	11.80	63.3%	12 m	12.9%
plots	acres	sellable	all roads	open space

SHEET INDEX

01	**Location and approach**	From the Jalkoti–Maheshwar road to the colony ga…	A3 · 1:3500
02	**Colony layout**	Plot numbers and areas, roads, open space, servi…	A3 · 1:1400
03	**Dimensioned layout and schedules**	Whole colony with every dimension, plus all the …	A0 · 1:500
04	**Dimension sheet – west half**	River-front plots R6–R19, S3 and S4 blocks, the …	A3 · 1:700
05	**Dimension sheet – east half**	R1–R5, S1, S2, S5 and the gate area	A3 · 1:700
06	**Plot dimension schedule**	Area, frontage and every side of all 62 plots	A3 · —
07	**Roads, medians, open space, services**	Widths, lengths, cross-sections, area statement	A3 · —

JALKOTI COLONY · MAHESHWAR

Khargone, Madhya Pradesh

Survey Drg SU/10/01 · 23.325 acres

Drawing set – cover and index


Dimensioned layout drawings for the colony

Cover · A3 portrait

Scale as noted · 12 Nov 2026 Concept

01 LOCATION AND APPROACH

From the Jalkoti–Maheshwar road to the colony gate

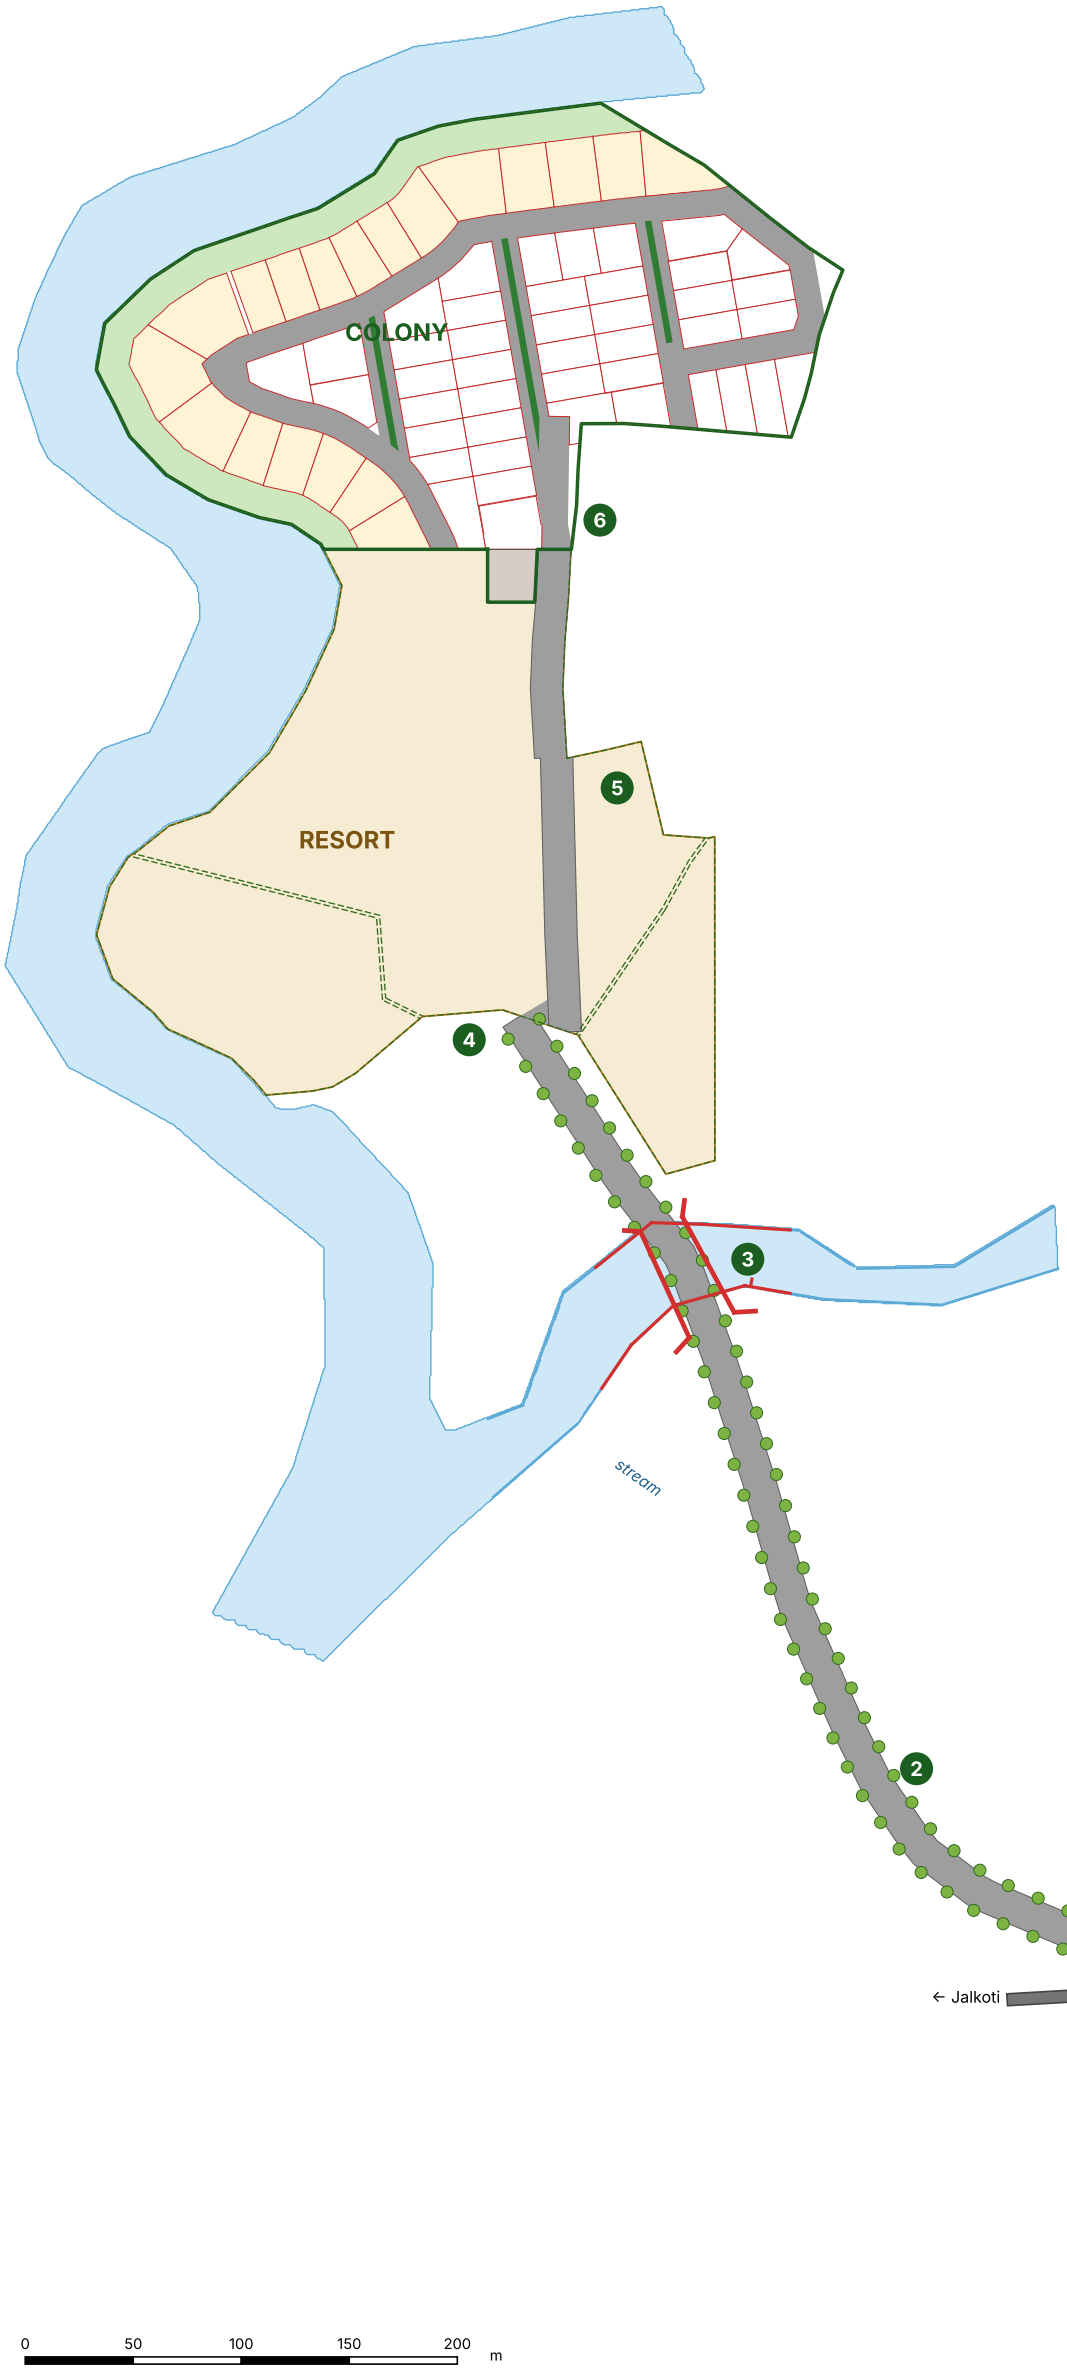

THE ROUTE FROM THE MAIN ROAD


1. **Existing Jalkoti–Maheshwar road**
   main road, about 5.5 m wide
2. **Approach road · about 553 m**
   15 m ROW, 9 m carriageway, avenue trees
3. **Bridge over the stream**
   on the approach road, as surveyed
4. **Main entry**
   entry splay joins the access road
5. **Access road · about 223 m**
   15 m, through the resort land
6. **Colony gate**
   62 plots inside; all roads 12 m

Main road → colony gate


about 800 m

ROAD SECTIONS (m)

Approach road (survey)

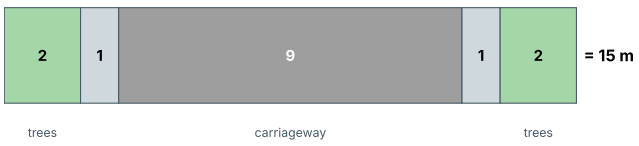

Access road

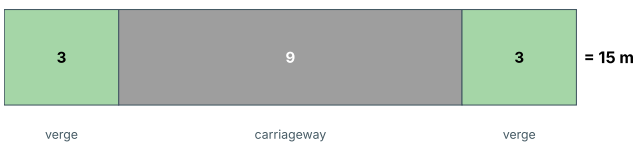

AREAS

- Site as surveyed: 23.325 acres
- Colony: 11.80 acres
- Resort: 11.63 acres

Dedicate the approach road and the access road as public roads before the colony application (BVN Rules 2(72), 38(6)).

Approach road, bridge, existing road and mandir traced from the survey (Drg SU/10/01, 1:1000).

JALKOTI COLONY · MAHESHWAR Khargone, Madhya Pradesh Survey Drg SU/10/01 · 23.325 acres	**Location and approach** From the Jalkoti–Maheshwar road to the colony gate	**Sheet 1 of 7 · A3 portrait** Scale 1:3500 · 12 Nov 2026 Concept

02 COLONY LAYOUT

Plot numbers and areas, roads, open space, services



AREA STATEMENT

Use	No.	sq ft	m²	%
River-front plots	19	134,511	12,496	26.2
Villa plots	43	190,872	17,732	37.1
Roads – carriageway and verges		109,048	10,131	21.2
Garden medians (road land)		6,821	634	1.3
Riverside garden (open space)		66,261	6,156	12.9
Services plot		5,906	549	1.1
Landscaped corners		4,516	420	0.9
7 ft walkway		712	66	0.1
Total colony	62	513,947	47,747	100.0

SELLABLE 325,383 sq ft

7.47 acres · 63.3% of the colony

PLOTS

- 19 river-front plots, 5,275–10,853 sq ft
- 43 villa plots, 3,616–6,489 sq ft
- Typical villa plot 45 × 90 ft (4,050 sq ft)
- Every frontage above 12 m (BVN 53)

ROADS – ALL 12 m

- RD river drive · S1 east street
- S2, S3, S4 garden streets (3 m median)
- S5 link road joins S1 to S2
- Access road 15 m · 223 m to the main entry
- Dead ends: S2 stub, RD south (turning space)

River-front plot
Villa plot
Road (right of way)
Garden median (road land)
Riverside garden (open space)
Landscaped corner
7 ft walkway
Services plot
T = turning space 12 × 11 m
Resort
Colony boundary

03 DIMENSIONED LAYOUT AND SCHEDULES

Whole colony with every dimension, plus all the tables



HOW TO READ THIS SHEET

- Blue figures inside each plot: side lengths in feet (1 m = 3.281 ft)
- "arc": curved side, measured along the curve
- Bold: plot number and area in sq ft
- Blue arrows across roads: right-of-way width (m)
- White text on green: garden median width × length (m)
- Green arrows: riverside garden width (m)
- Dark green outside the boundary: boundary lengths (m)
- T: turning space 12 × 11 m at a dead end

SETBACKS (BVN 2012, Rule 56)

- Front 3.6 m on a 12 m road · rear 3.0 m · sides 3.0 m each (detached)
- River-front plots: 15 m garden from the stream edge + 3 m rear setback

ACCURACY

- Measured from the survey scan (Drg SU/10/01) calibrated to its surveyed areas: ±0.5 m
- Redraw on the CAD survey and verify on site before marking out or selling

ROADS

Road	Runs	ROW	Length m	Area m²
RD	along the river-front plots, from S1 round the bend to the south end	12 m	456	4,833
S1	from RD (via the bend at V5/V7) down the east boundary to S5	12 m	70	577
S2	from RD south to the boundary (V38 stub)	12 m	111	1,163
S3	from RD south to the colony gate	12 m	155	1,258
S4	from RD south to the RD south loop	12 m	64	729
S5	joins S1 to S2 along V16/V18 (new)	12 m	68	760
Access road	colony gate to the main entry	15 m	223	3,334
Approach road	Main road → bridge → main entry (survey)	15 m	553	8,384

GARDEN MEDIANS

Median	Width	Length m	Area m²
On S2	3.0 m	61.0	172
On S3	3.0 m	100.3	277
On S4	3.0 m	63.9	185

AREA STATEMENT

Use	No.	sq ft	m²	%
River-front plots	19	134,511	12,496	26.2
Villa plots	43	190,872	17,732	37.1
Roads – carriageway and verges		109,048	10,131	21.2
Garden medians (road land)		6,821	634	1.3
Riverside garden (open space)		66,261	6,156	12.9
Services plot		5,906	549	1.1
Landscaped corners		4,516	420	0.9
7 ft walkway		712	66	0.1
Total colony	62	513,947	47,747	100.0

SELLABLE 325,383 sq ft · 7.47 acres · 63.3%

PLOT DIMENSION SCHEDULE

Sides clockwise from the front (main road side) · road sides carry the road name · "arc" = curved side

Plot	Type	sq ft	m²	Frontage	Sides in feet (clockwise from the front) – metres on Sheet 6
R1	River-front	9,875	917.4	22.6 m · RD	74.3 RD arc · 103.8 · 125.2 arc · 98.9
R2	River-front	7,170	666.1	22.4 m · RD	73.4 RD · 98.9 · 71.5 · 98.9
R3	River-front	7,193	668.2	22.0 m · RD	72.3 RD · 98.9 · 73.1 · 99.3
R4	River-front	6,943	645.1	20.7 m · RD	68.1 RD · 99.3 · 72.3 · 99.1
R5	River-front	7,351	682.9	39.1 m · RD	128.2 RD arc · 99.1 · 9.6 · 152.2 arc
R6	River-front	5,352	497.2	18.3 m · RD	60.0 RD · 98.9 · 48.0 · 98.9
R7	River-front	5,488	509.8	18.8 m · RD	61.5 RD arc · 98.9 · 49.4 · 99.0
R8	River-front	5,275	490.1	16.1 m · RD	52.7 RD · 99.0 · 53.9 · 98.9
R9	River-front	7,505	697.2	24.0 m · RD	78.7 RD arc · 98.9 · 71.4 arc · 105.4 arc
R10	River-front	10,853	1,008.2	22.7 m · RD	74.5 RD arc · 103.4 · 144.6 arc · 98.9
R11	River-front	5,354	497.4	16.2 m · RD	53.2 RD · 99.1 · 55.0 · 98.9
R12	River-front	5,375	499.4	16.5 m · RD	54.1 RD · 98.9 · 54.5 · 98.9
R13	River-front	10,707	994.7	13.2 m · RD	33.1 RD · 99.4 · 99.2 arc · 40.4 · 29.6 · 103.4 · 10.1 RD
R14	River-front	9,805	910.9	22.7 m · RD	74.4 RD arc · 99.4 · 123.9 arc · 99.4
R15	River-front	5,761	535.2	15.8 m · RD	51.7 RD · 99.4 · 64.7 · 99.4
R16	River-front	6,211	577.0	19.3 m · RD	63.3 RD arc · 99.0 · 61.9 · 99.4
R17	River-front	6,152	571.5	22.9 m · RD	75.2 RD arc · 99.1 · 49.1 arc · 99.0
R18	River-front	6,151	571.4	25.4 m · RD	83.4 RD arc · 98.9 · 40.9 arc · 99.1
R19	River-front	5,989	556.4	27.0 m · RD	88.4 RD · 109.8 · 31.4 · 98.9
V1	Villa	5,452	506.5	54.6 m · RD+S3	76.8 S3 · 90.0 · 35.8 · 75.2 RD arc · 27.3 RD
V2	Villa	4,206	390.8	40.1 m · RD+S3	75.1 S3 · 56.6 RD · 72.5 · 56.9
V3	Villa	4,207	390.8	18.0 m · RD	59.0 RD · 69.7 · 59.1 · 72.5
V4	Villa	4,354	404.5	39.7 m · RD+S2	66.0 S2 · 64.0 · 69.7 · 64.1 RD
V5	Villa	6,081	564.9	58.7 m · RD+S2	95.2 RD arc · 36.0 RD · 42.5 arc · 87.7 · 61.5 S2
V6	Villa	4,050	376.3	13.7 m · S2	45.0 S2 · 90.0 · 45.0 · 90.0
V7	Villa	4,119	382.7	29.5 m · S1	89.8 S1 · 6.9 S1 · 88.7 · 45.3 · 40.3
V8	Villa	5,659	525.7	43.2 m · RD+S4	96.9 RD · 80.8 · 90.0 · 45.0 S4
V9	Villa	4,050	376.3	13.7 m · S3	45.0 S3 · 90.0 · 45.0 · 90.0
V10	Villa	4,050	376.3	13.7 m · S3	45.0 S3 · 90.0 · 45.0 · 90.0
V11	Villa	4,050	376.2	13.7 m · S3	45.0 S3 · 90.0 · 45.0 · 90.0
V12	Villa	4,050	376.2	13.7 m · S3	45.0 S3 · 90.0 · 45.0 · 90.0
V13	Villa	4,050	376.2	13.7 m · S2	45.0 S2 · 90.0 · 45.0 · 90.0
V14	Villa	4,050	376.2	13.7 m · S2	45.0 S2 · 90.0 · 45.0 · 90.0
V15	Villa	4,050	376.3	13.7 m · S2	45.0 S2 · 90.0 · 45.0 · 90.0
V16	Villa	4,050	376.3	41.1 m · S2+S5	90.0 S5 · 45.0 S2 · 90.0 · 45.0
V17	Villa	4,050	376.3	13.7 m · S1	45.0 S1 · 90.0 · 45.0 · 90.0
V18	Villa	3,949	366.9	38.8 m · S1+S5	79.7 S5 · 45.0 · 90.0 · 47.6 S1 arc
V19	Villa	5,793	538.2	68.0 m · RD	103.2 RD arc · 28.3 RD · 91.4 RD · 92.8
V20	Villa	6,414	595.8	51.8 m · RD+S4	91.2 RD · 78.7 S4 · 90.0 · 64.0
V21	Villa	4,050	376.3	13.7 m · S4	45.0 S4 · 90.0 · 45.0 · 90.0
V22	Villa	4,050	376.3	13.7 m · S4	45.0 S4 · 90.0 · 45.0 · 90.0
V23	Villa	4,050	376.3	13.7 m · S3	45.0 S3 · 90.0 · 45.0 · 90.0
V24	Villa	4,050	376.3	13.7 m · S3	45.0 S3 · 90.0 · 45.0 · 90.0
V25	Villa	4,050	376.2	13.7 m · S3	45.0 S3 · 90.0 · 45.0 · 90.0
V26	Villa	4,050	376.2	13.7 m · S3	45.0 S3 · 90.0 · 45.0 · 90.0
V27	Villa	4,050	376.2	13.7 m · S2	45.0 S2 · 90.0 · 45.0 · 90.0
V28	Villa	4,050	376.2	13.7 m · S2	45.0 S2 · 90.0 · 45.0 · 90.0
V29	Villa	3,835	356.3	38.7 m · S2+S5	84.2 S2 · 42.7 S5 · 95.7 · 44.1
V30	Villa	4,592	426.6	13.8 m · S5	45.2 S5 · 107.7 · 46.7 · 95.7
V31	Villa	5,133	476.9	13.8 m · S5	45.2 S5 · 119.7 · 46.7 · 107.7
V32	Villa	4,050	376.3	13.7 m · S4	45.0 S4 · 90.0 · 45.0 · 90.0
V33	Villa	4,050	376.3	13.7 m · S4	45.0 S4 · 90.0 · 45.0 · 90.0
V34	Villa	3,616	335.9	15.2 m · RD	49.9 RD arc · 90.0 · 45.0 · 70.0
V35	Villa	4,050	376.3	13.7 m · S3	45.0 S3 · 90.0 · 45.0 · 90.0
V36	Villa	4,050	376.3	13.7 m · S3	45.0 S3 · 90.0 · 45.0 · 90.0
V37	Villa	4,181	388.5	28.8 m · S3	43.0 S3 · 31.5 S3 · 20.1 S3 · 90.5 · 9.2 · 47.5 · 10.3 · 43.8 · 29.5 · 16.5
V38	Villa	4,522	420.1	20.4 m · S2	66.8 S2 · 82.1 · 47.5 · 79.8
V39	Villa	5,870	545.4	33.3 m · RD	109.2 RD arc · 70.0 · 112.5 · 41.8
V40	Villa	4,050	376.3	13.7 m · S3	45.0 S3 · 90.0 · 45.0 · 90.0
V41	Villa	6,489	602.9	25.0 m · S3	82.2 S3 arc · 84.6 · 66.8 · 88.0
V42	Villa	4,911	456.2	50.4 m · RD+S4	91.6 RD arc · 28.2 · 89.8 · 73.6 S4 · 15.7
V43	Villa	4,340	403.2	19.3 m · S5	63.3 S5 · 134.5 arc · 4.6 · 119.7

JALKOTI COLONY · MAHESHWAR

Khargone, Madhya Pradesh

Survey Drg SU/10/01 · 23.325 acres

Dimensioned layout and schedules

Whole colony with every dimension, plus all the tables

Sheet 3 of 7 · A0 portrait

Scale 1:500 · 12 Nov 2026

Concept

04 DIMENSION SHEET – WEST HALF

River-front plots R6–R19, S3 and S4 blocks, the bend



JALKOTI COLONY · MAHESHWAR Khargone, Madhya Pradesh Survey Drg SU/10/01 · 23.325 acres	**Dimension sheet – west half** River-front plots R6–R19, S3 and S4 blocks, the bend	**Sheet 4 of 7 · A3 portrait** Scale 1:700 · 12 Nov 2026 Concept

05 DIMENSION SHEET – EAST HALF

R1–R5, S1, S2, S5 and the gate area



JALKOTI COLONY · MAHESHWAR

Khargone, Madhya Pradesh

Survey Drg SU/10/01 · 23.325 acres

Dimension sheet – east half

R1–R5, S1, S2, S5 and the gate area

Sheet 5 of 7 · A3 portrait

Scale 1:700 · 12 Nov 2026 Concept

06 PLOT DIMENSION SCHEDULE

Area, frontage and every side of all 62 plots

Sides clockwise from the front (main road side). Road sides carry the road name; "arc" = curved side measured along the curve.

Plot	Type	sq ft	m²	Frontage	Sides in feet	Sides in metres
R1	River-front	9,875	917.4	22.6 m · RD	74.3 RD arc · 103.8 · 125.2 arc · 98.9	22.65 RD arc · 31.64 · 38.17 arc · 30.15
R2	River-front	7,170	666.1	22.4 m · RD	73.4 RD · 98.9 · 71.5 · 98.9	22.37 RD · 30.15 · 21.78 · 30.14
R3	River-front	7,193	668.2	22.0 m · RD	72.3 RD · 98.9 · 73.1 · 99.3	22.04 RD · 30.14 · 22.27 · 30.25
R4	River-front	6,943	645.1	20.7 m · RD	68.1 RD · 99.3 · 72.3 · 99.1	20.74 RD · 30.25 · 22.03 · 30.21
R5	River-front	7,351	682.9	39.1 m · RD	128.2 RD arc · 99.1 · 9.6 · 152.2 arc	39.08 RD arc · 30.21 · 2.93 · 46.39 arc
R6	River-front	5,352	497.2	18.3 m · RD	60.0 RD · 98.9 · 48.0 · 98.9	18.28 RD · 30.15 · 14.64 · 30.14
R7	River-front	5,488	509.8	18.8 m · RD	61.5 RD arc · 98.9 · 49.4 · 99.0	18.76 RD arc · 30.14 · 15.04 · 30.18
R8	River-front	5,275	490.1	16.1 m · RD	52.7 RD · 99.0 · 53.9 · 98.9	16.07 RD · 30.18 · 16.42 · 30.14
R9	River-front	7,505	697.2	24.0 m · RD	78.7 RD arc · 98.9 · 71.4 arc · 105.4 arc	23.99 RD arc · 30.13 · 21.76 arc · 32.11 arc
R10	River-front	10,853	1,008.2	22.7 m · RD	74.5 RD arc · 103.4 · 144.6 arc · 98.9	22.71 RD arc · 31.52 · 44.09 arc · 30.16
R11	River-front	5,354	497.4	16.2 m · RD	53.2 RD · 99.1 · 55.0 · 98.9	16.22 RD · 30.19 · 16.75 · 30.15
R12	River-front	5,375	499.4	16.5 m · RD	54.1 RD · 98.9 · 54.5 · 98.9	16.50 RD · 30.15 · 16.60 · 30.15
R13	River-front	10,707	994.7	13.2 m · RD	33.1 RD · 99.4 · 99.2 arc · 40.4 · 29.6 · 103.4 · 10.1 RD	10.09 RD · 30.29 · 30.24 arc · 12.32 · 9.03 · 31.52 · 3.09 RD
R14	River-front	9,805	910.9	22.7 m · RD	74.4 RD arc · 99.4 · 123.9 arc · 99.4	22.67 RD arc · 30.29 · 37.76 arc · 30.29
R15	River-front	5,761	535.2	15.8 m · RD	51.7 RD · 99.4 · 64.7 · 99.4	15.77 RD · 30.29 · 19.71 · 30.29
R16	River-front	6,211	577.0	19.3 m · RD	63.3 RD arc · 99.0 · 61.9 · 99.4	19.31 RD arc · 30.18 · 18.86 · 30.29
R17	River-front	6,152	571.5	22.9 m · RD	75.2 RD arc · 99.1 · 49.1 arc · 99.0	22.91 RD arc · 30.19 · 14.97 arc · 30.18
R18	River-front	6,151	571.4	25.4 m · RD	83.4 RD arc · 98.9 · 40.9 arc · 99.1	25.42 RD arc · 30.15 · 12.48 arc · 30.19
R19	River-front	5,989	556.4	27.0 m · RD	88.4 RD · 109.8 · 31.4 · 98.9	26.96 RD · 33.46 · 9.56 · 30.15
V1	Villa	5,452	506.5	54.6 m · RD+S3	76.8 S3 · 90.0 · 35.8 · 75.2 RD arc · 27.3 RD	23.41 S3 · 27.43 · 10.91 · 22.91 RD arc · 8.32 RD
V2	Villa	4,206	390.8	40.1 m · RD+S3	75.1 S3 · 56.6 RD · 72.5 · 56.9	22.89 S3 · 17.26 RD · 22.09 · 17.35
V3	Villa	4,207	390.8	18.0 m · RD	59.0 RD · 69.7 · 59.1 · 72.5	17.98 RD · 21.26 · 18.00 · 22.08
V4	Villa	4,354	404.5	39.7 m · RD+S2	66.0 S2 · 64.0 · 69.7 · 64.1 RD	20.11 S2 · 19.51 · 21.26 · 19.54 RD
V5	Villa	6,081	564.9	58.7 m · RD+S2	95.2 RD arc · 36.0 RD · 42.5 arc · 87.7 · 61.5 S2	29.02 RD arc · 10.96 RD · 12.94 arc · 26.72 · 18.73 S2
V6	Villa	4,050	376.3	13.7 m · S2	45.0 S2 · 90.0 · 45.0 · 90.0	13.72 S2 · 27.43 · 13.72 · 27.43
V7	Villa	4,119	382.7	29.5 m · S1	89.8 S1 · 6.9 S1 · 88.7 · 45.3 · 40.3	27.36 S1 · 2.11 S1 · 27.03 · 13.79 · 12.28
V8	Villa	5,659	525.7	43.2 m · RD+S4	96.9 RD · 80.8 · 90.0 · 45.0 S4	29.52 RD · 24.63 · 27.43 · 13.72 S4
V9	Villa	4,050	376.3	13.7 m · S3	45.0 S3 · 90.0 · 45.0 · 90.0	13.72 S3 · 27.43 · 13.72 · 27.43
V10	Villa	4,050	376.3	13.7 m · S3	45.0 S3 · 90.0 · 45.0 · 90.0	13.72 S3 · 27.43 · 13.72 · 27.43
V11	Villa	4,050	376.2	13.7 m · S3	45.0 S3 · 90.0 · 45.0 · 90.0	13.72 S3 · 27.43 · 13.72 · 27.43
V12	Villa	4,050	376.2	13.7 m · S3	45.0 S3 · 90.0 · 45.0 · 90.0	13.72 S3 · 27.43 · 13.72 · 27.43
V13	Villa	4,050	376.2	13.7 m · S2	45.0 S2 · 90.0 · 45.0 · 90.0	13.72 S2 · 27.43 · 13.72 · 27.43
V14	Villa	4,050	376.2	13.7 m · S2	45.0 S2 · 90.0 · 45.0 · 90.0	13.72 S2 · 27.43 · 13.72 · 27.43
V15	Villa	4,050	376.3	13.7 m · S2	45.0 S2 · 90.0 · 45.0 · 90.0	13.72 S2 · 27.43 · 13.72 · 27.43
V16	Villa	4,050	376.3	41.1 m · S2+S5	90.0 S5 · 45.0 S2 · 90.0 · 45.0	27.43 S5 · 13.72 S2 · 27.43 · 13.72
V17	Villa	4,050	376.3	13.7 m · S1	45.0 S1 · 90.0 · 45.0 · 90.0	13.72 S1 · 27.43 · 13.72 · 27.43
V18	Villa	3,949	366.9	38.8 m · S1+S5	79.7 S5 · 45.0 · 90.0 · 47.6 S1 arc	24.29 S5 · 13.72 · 27.43 · 14.50 S1 arc
V19	Villa	5,793	538.2	68.0 m · RD	103.2 RD arc · 28.3 RD · 91.4 RD · 92.8	31.46 RD arc · 8.64 RD · 27.86 RD · 28.30
V20	Villa	6,414	595.8	51.8 m · RD+S4	91.2 RD · 78.7 S4 · 90.0 · 64.0	27.79 RD · 23.98 S4 · 27.43 · 19.51
V21	Villa	4,050	376.3	13.7 m · S4	45.0 S4 · 90.0 · 45.0 · 90.0	13.72 S4 · 27.43 · 13.72 · 27.43
V22	Villa	4,050	376.3	13.7 m · S4	45.0 S4 · 90.0 · 45.0 · 90.0	13.72 S4 · 27.43 · 13.72 · 27.43
V23	Villa	4,050	376.3	13.7 m · S3	45.0 S3 · 90.0 · 45.0 · 90.0	13.72 S3 · 27.43 · 13.72 · 27.43
V24	Villa	4,050	376.3	13.7 m · S3	45.0 S3 · 90.0 · 45.0 · 90.0	13.72 S3 · 27.43 · 13.72 · 27.43
V25	Villa	4,050	376.2	13.7 m · S3	45.0 S3 · 90.0 · 45.0 · 90.0	13.72 S3 · 27.43 · 13.72 · 27.43
V26	Villa	4,050	376.2	13.7 m · S3	45.0 S3 · 90.0 · 45.0 · 90.0	13.72 S3 · 27.43 · 13.72 · 27.43
V27	Villa	4,050	376.2	13.7 m · S2	45.0 S2 · 90.0 · 45.0 · 90.0	13.72 S2 · 27.43 · 13.72 · 27.43
V28	Villa	4,050	376.2	13.7 m · S2	45.0 S2 · 90.0 · 45.0 · 90.0	13.72 S2 · 27.43 · 13.72 · 27.43
V29	Villa	3,835	356.3	38.7 m · S2+S5	84.2 S2 · 42.7 S5 · 95.7 · 44.1	25.65 S2 · 13.00 S5 · 29.17 · 13.45
V30	Villa	4,592	426.6	13.8 m · S5	45.2 S5 · 107.7 · 46.7 · 95.7	13.76 S5 · 32.83 · 14.24 · 29.17
V31	Villa	5,133	476.9	13.8 m · S5	45.2 S5 · 119.7 · 46.7 · 107.7	13.76 S5 · 36.48 · 14.24 · 32.83
V32	Villa	4,050	376.3	13.7 m · S4	45.0 S4 · 90.0 · 45.0 · 90.0	13.72 S4 · 27.43 · 13.72 · 27.43
V33	Villa	4,050	376.3	13.7 m · S4	45.0 S4 · 90.0 · 45.0 · 90.0	13.72 S4 · 27.43 · 13.72 · 27.43
V34	Villa	3,616	335.9	15.2 m · RD	49.9 RD arc · 90.0 · 45.0 · 70.0	15.20 RD arc · 27.43 · 13.72 · 21.33
V35	Villa	4,050	376.3	13.7 m · S3	45.0 S3 · 90.0 · 45.0 · 90.0	13.72 S3 · 27.43 · 13.72 · 27.43
V36	Villa	4,050	376.3	13.7 m · S3	45.0 S3 · 90.0 · 45.0 · 90.0	13.72 S3 · 27.43 · 13.72 · 27.43
V37	Villa	4,181	388.5	28.8 m · S3	43.0 S3 · 31.5 S3 · 20.1 S3 · 90.5 · 9.2 · 47.5 · 10.3 · 43.8 · 29.5 · 16.5	13.11 S3 · 9.59 S3 · 6.12 S3 · 27.57 · 2.82 · 14.48 · 3.15 · 13.34 · 8.98 · 5.03
V38	Villa	4,522	420.1	20.4 m · S2	66.8 S2 · 82.1 · 47.5 · 79.8	20.35 S2 · 25.03 · 14.48 · 24.32
V39	Villa	5,870	545.4	33.3 m · RD	109.2 RD arc · 70.0 · 112.5 · 41.8	33.28 RD arc · 21.33 · 34.28 · 12.74
V40	Villa	4,050	376.3	13.7 m · S3	45.0 S3 · 90.0 · 45.0 · 90.0	13.72 S3 · 27.43 · 13.72 · 27.43
V41	Villa	6,489	602.9	25.0 m · S3	82.2 S3 arc · 84.6 · 66.8 · 88.0	25.05 S3 arc · 25.78 · 20.35 · 26.83
V42	Villa	4,911	456.2	50.4 m · RD+S4	91.6 RD arc · 28.2 · 89.8 · 73.6 S4 · 15.7	27.91 RD arc · 8.59 · 27.37 · 22.44 S4 · 4.77
V43	Villa	4,340	403.2	19.3 m · S5	63.3 S5 · 134.5 arc · 4.6 · 119.7	19.30 S5 · 40.99 arc · 1.39 · 36.48

Total 62 plots · 325,383 sq ft (30,229 m²) · 63.3% of the colony

Measured from the survey scan (±0.5 m) – verify on site.

07 ROADS, MEDIANS, OPEN SPACE, SERVICES

Widths, lengths, cross-sections, area statement

ROADS

Road	Runs	ROW	Length m	Area m²
RD	along the river-front plots, from S1 round the bend to the south end	12 m	456	4,833
S1	from RD (via the bend at V5/V7) down the east boundary to S5	12 m	70	577
S2	from RD south to the boundary (V38 stub)	12 m	111	1,163
S3	from RD south to the colony gate	12 m	155	1,258
S4	from RD south to the RD south loop	12 m	64	729
S5	joins S1 to S2 along V16/V18 (new)	12 m	68	760
Access road	colony gate to the main entry	15 m	223	3,334
Approach road	Main road → bridge → main entry (survey)	15 m	553	8,384
Entry splay	Approach road to access road at the main entry	—	—	78
Existing road	Jalkoti ← main road → Maheshwar (survey)	5.5 m	—	—

Lengths along the centre-line, junctions counted once. Farthest plot (V43) is 360 m from the colony gate (BVN 38: 12 m roads up to 400 m).

ROAD CROSS-SECTIONS (metres)

12 m plain road – RD, S1, S5, gate road



15 m access road – through the resort



12 m garden street – S2, S3, S4



15 m approach road – survey section



GARDEN MEDIANS

Median	Width m	Length m	Area m²	Note
Median on S2	3.0	61.0	172	stops 4 m short of junctions
Median on S3	3.0	100.3	277	stops 4 m short of junctions
Median on S4	3.0	63.9	185	stops 4 m short of junctions
Total		225.2	634	road land, not open space

OPEN SPACE, WALKWAY, SERVICES

Item	Dimensions	Area m²
Riverside garden	15 m wide · 460 m along plots	6,156
7 ft walkway	2.13 × 31.3 m (R10/R11)	66
Services plot	24.5 × 23.2 m at the gate	549
STP	10.0 × 8.0 m	80
Tank + tubewell	7.0 × 7.0 m	49
Waste point	5.0 × 4.0 m	20
Turning spaces	2 × 12 × 11 m (in roads)	264
Landscaped corners	6 pieces	420

AREA STATEMENT – COLONY

Use	No.	sq ft	m²	%
River-front plots	19	134,511	12,496	26.2
Villa plots	43	190,872	17,732	37.1
Roads – carriageway and verges		109,048	10,131	21.2
Garden medians (road land)		6,821	634	1.3
Riverside garden (open space)		66,261	6,156	12.9
Services plot		5,906	549	1.1
Landscaped corners		4,516	420	0.9
7 ft walkway		712	66	0.1
Total colony	62	513,947	47,747	100.0

SELLABLE 325,383 sq ft = 7.47 acres = 63.3%

Plot sides in feet (1 m = 3.281 ft); everything else in metres. Measured from the survey scan (±0.5 m). Concept only.